


Инв. № подл.	Подпись и дата
Взам. инв. №	Инв. № дубл.
Подпись и дата	

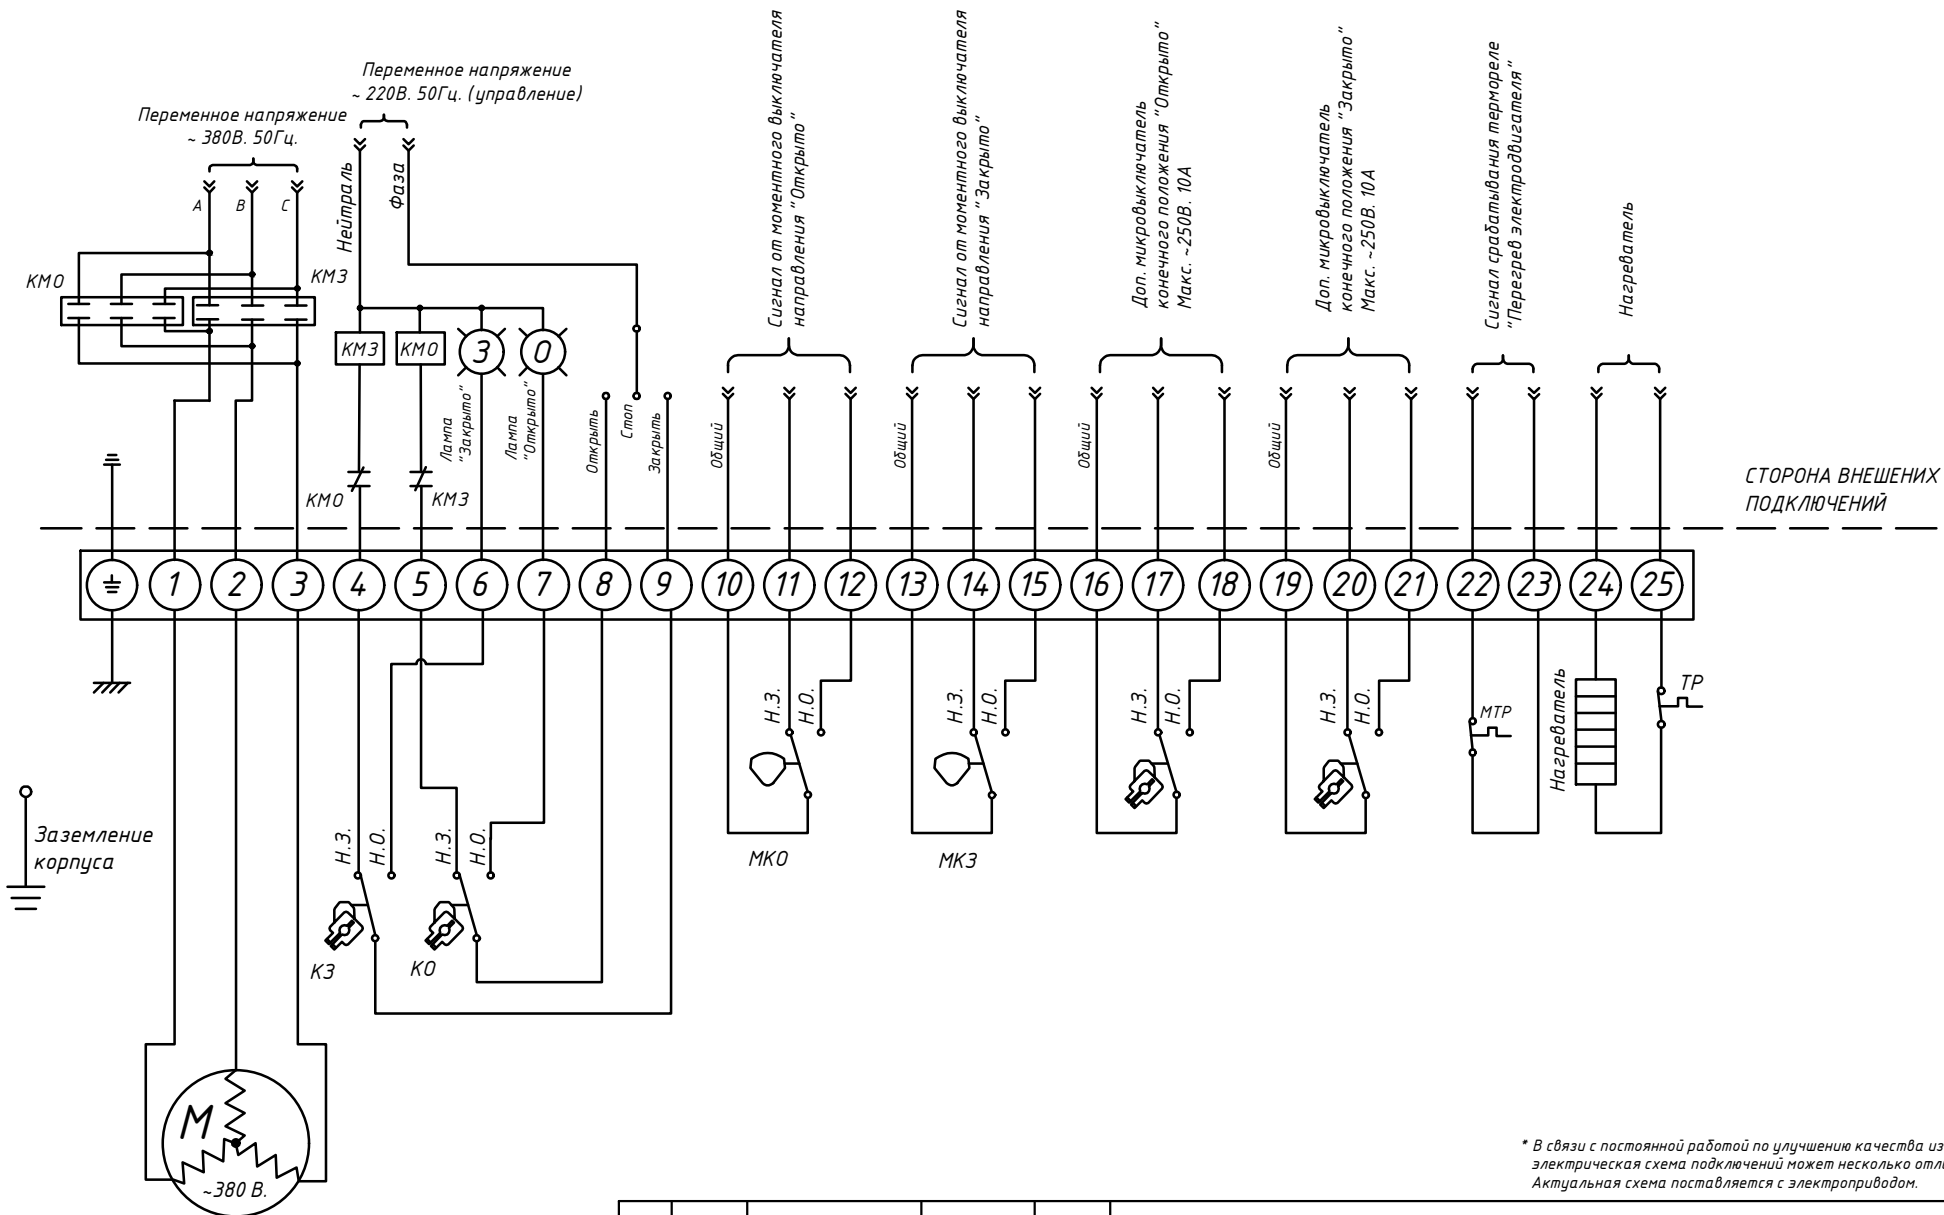

ТР - Термо-реле нагревателя
МТР - Термо-реле электродвигателя
М - Электродвигатель
МКЗ, МКО - Выключатели ограничителя момента
КЗ, К0 - Конечные выключатели
КМЗ, КМ0 - Контакторы

Изм.	Лист	№ докум.	Подп.	Дата	AR21-210-10		
Разраб.	Балашов К.В.			05.23			
Пров.					Электрическая схема электропривода AR21E Напряжение питания: 380В. (переменное). Режим: Закрывать / Открыть		
Н.контр.							
Утв.					Модельный ряд: AR21E.007-100		
					Стадия	Лист	Листов
					Р	1	1