


|              |                |              |              |              |
|--------------|----------------|--------------|--------------|--------------|
| Инв. № подл. | Подпись и дата | Взам. инв. № | Инв. № дубл. | Подп. и дата |
|              |                |              |              |              |

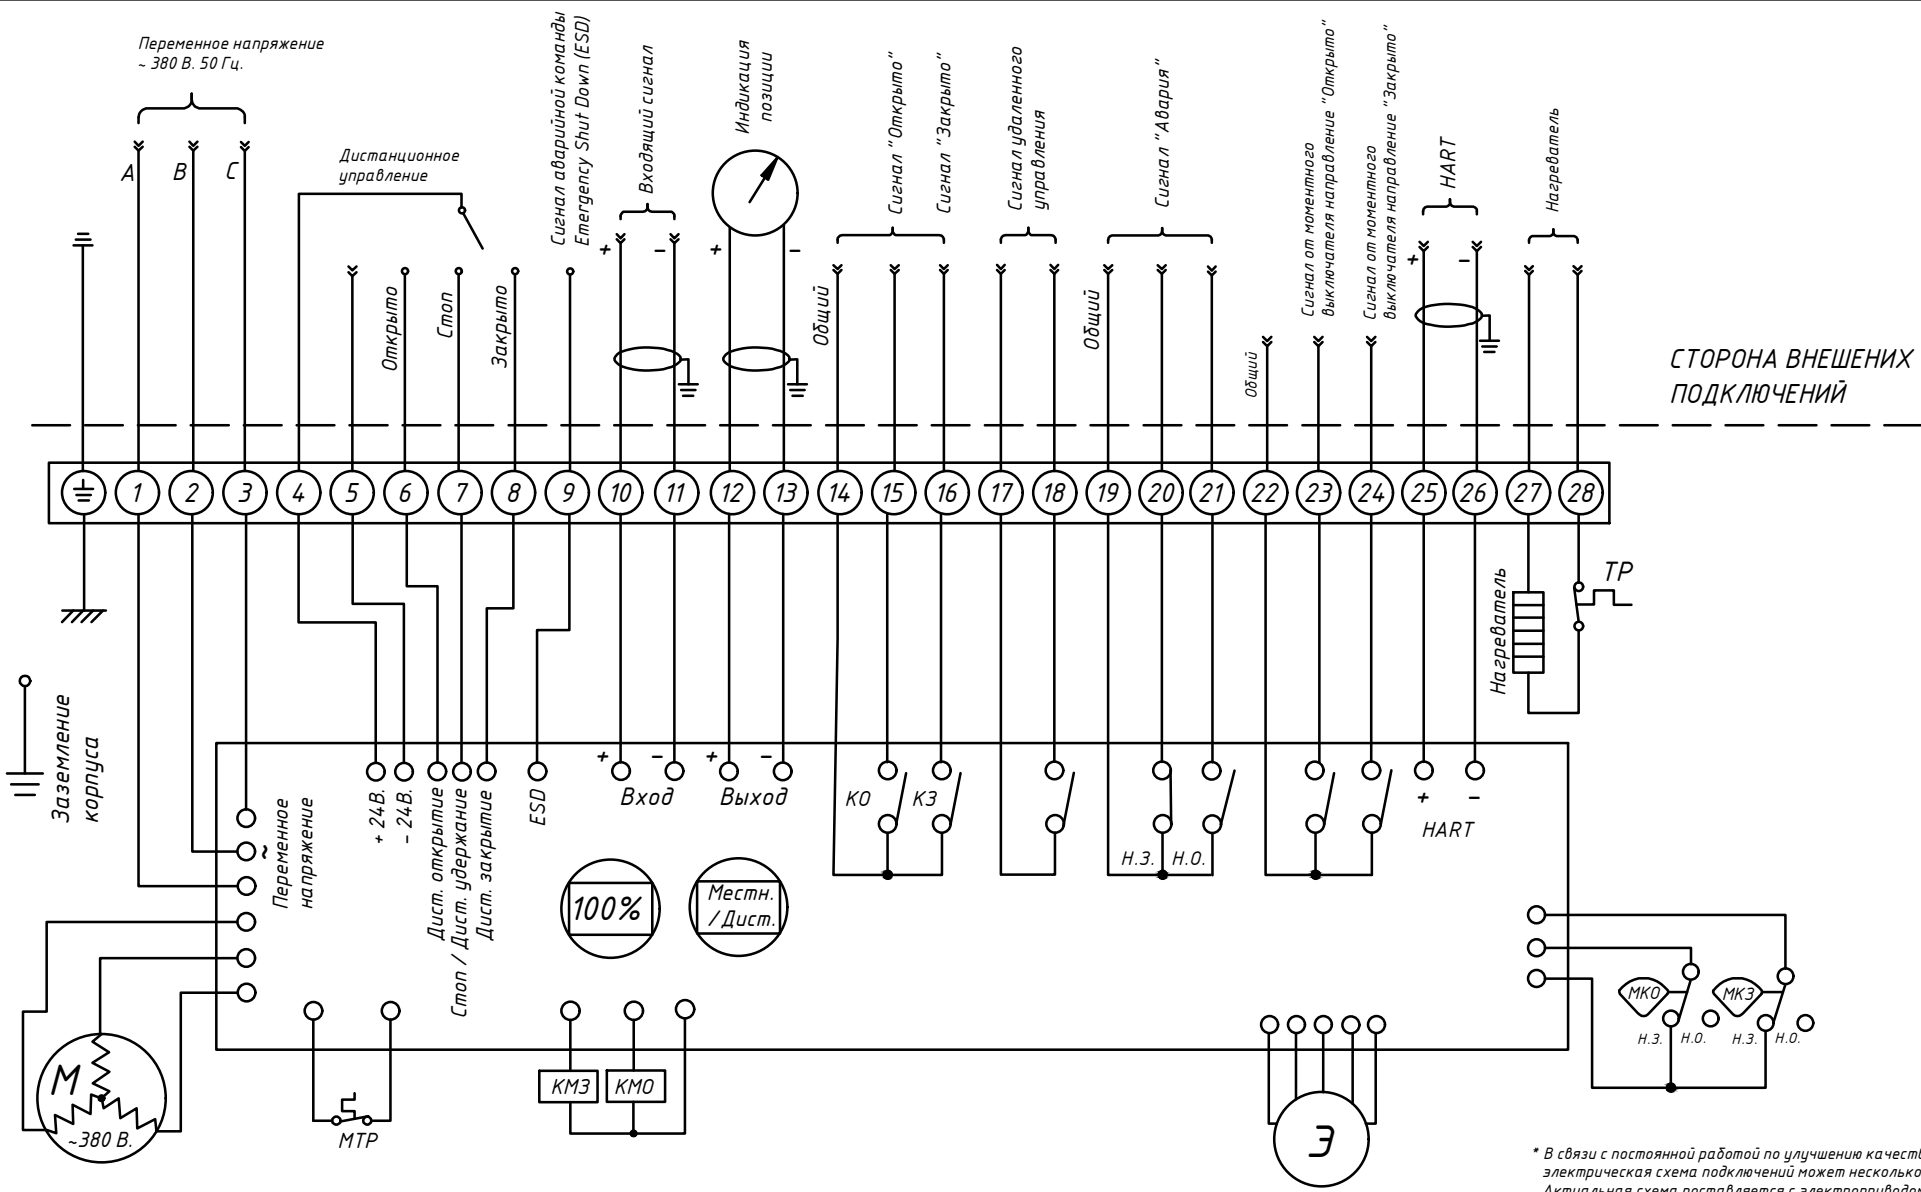

ТР - Термо-реле нагревателя  
МТР - Термо-реле электродвигателя  
М - Электродвигатель  
МКЗ, МКО - Выключатели ограничителя момента  
КЗ, КО - Конечные выключатели  
КМЗ, КМО - Контакторы  
Э - Энкодер

|          |              |          |       |       |
|----------|--------------|----------|-------|-------|
| Изм.     | Лист         | № докум. | Подп. | Дата  |
| Разраб.  | Балашов К.В. |          |       | 05.23 |
| Пров.    |              |          |       |       |
| Н.контр. |              |          |       |       |
| Утв.     |              |          |       |       |

# AR21E-28C-10

Электрическая схема электропривода AR21E  
Напряжение питания: 380В. (переменное).  
Режим: Интеллектуальный модуль INT/N

Протокол HART  
Модельный ряд: AR21E.007-100

|        |      |        |
|--------|------|--------|
| Стадия | Лист | Листов |
| Р      | 1    | 1      |

Формат А4

\* В связи с постоянной работой по улучшению качества изделий, электрическая схема подключений может несколько отличаться. Актуальная схема поставляется с электроприводом.