


Инв. № подл.	Подпись и дата	Взам. инв. №	Инв. № дубл.	Подп. и дата

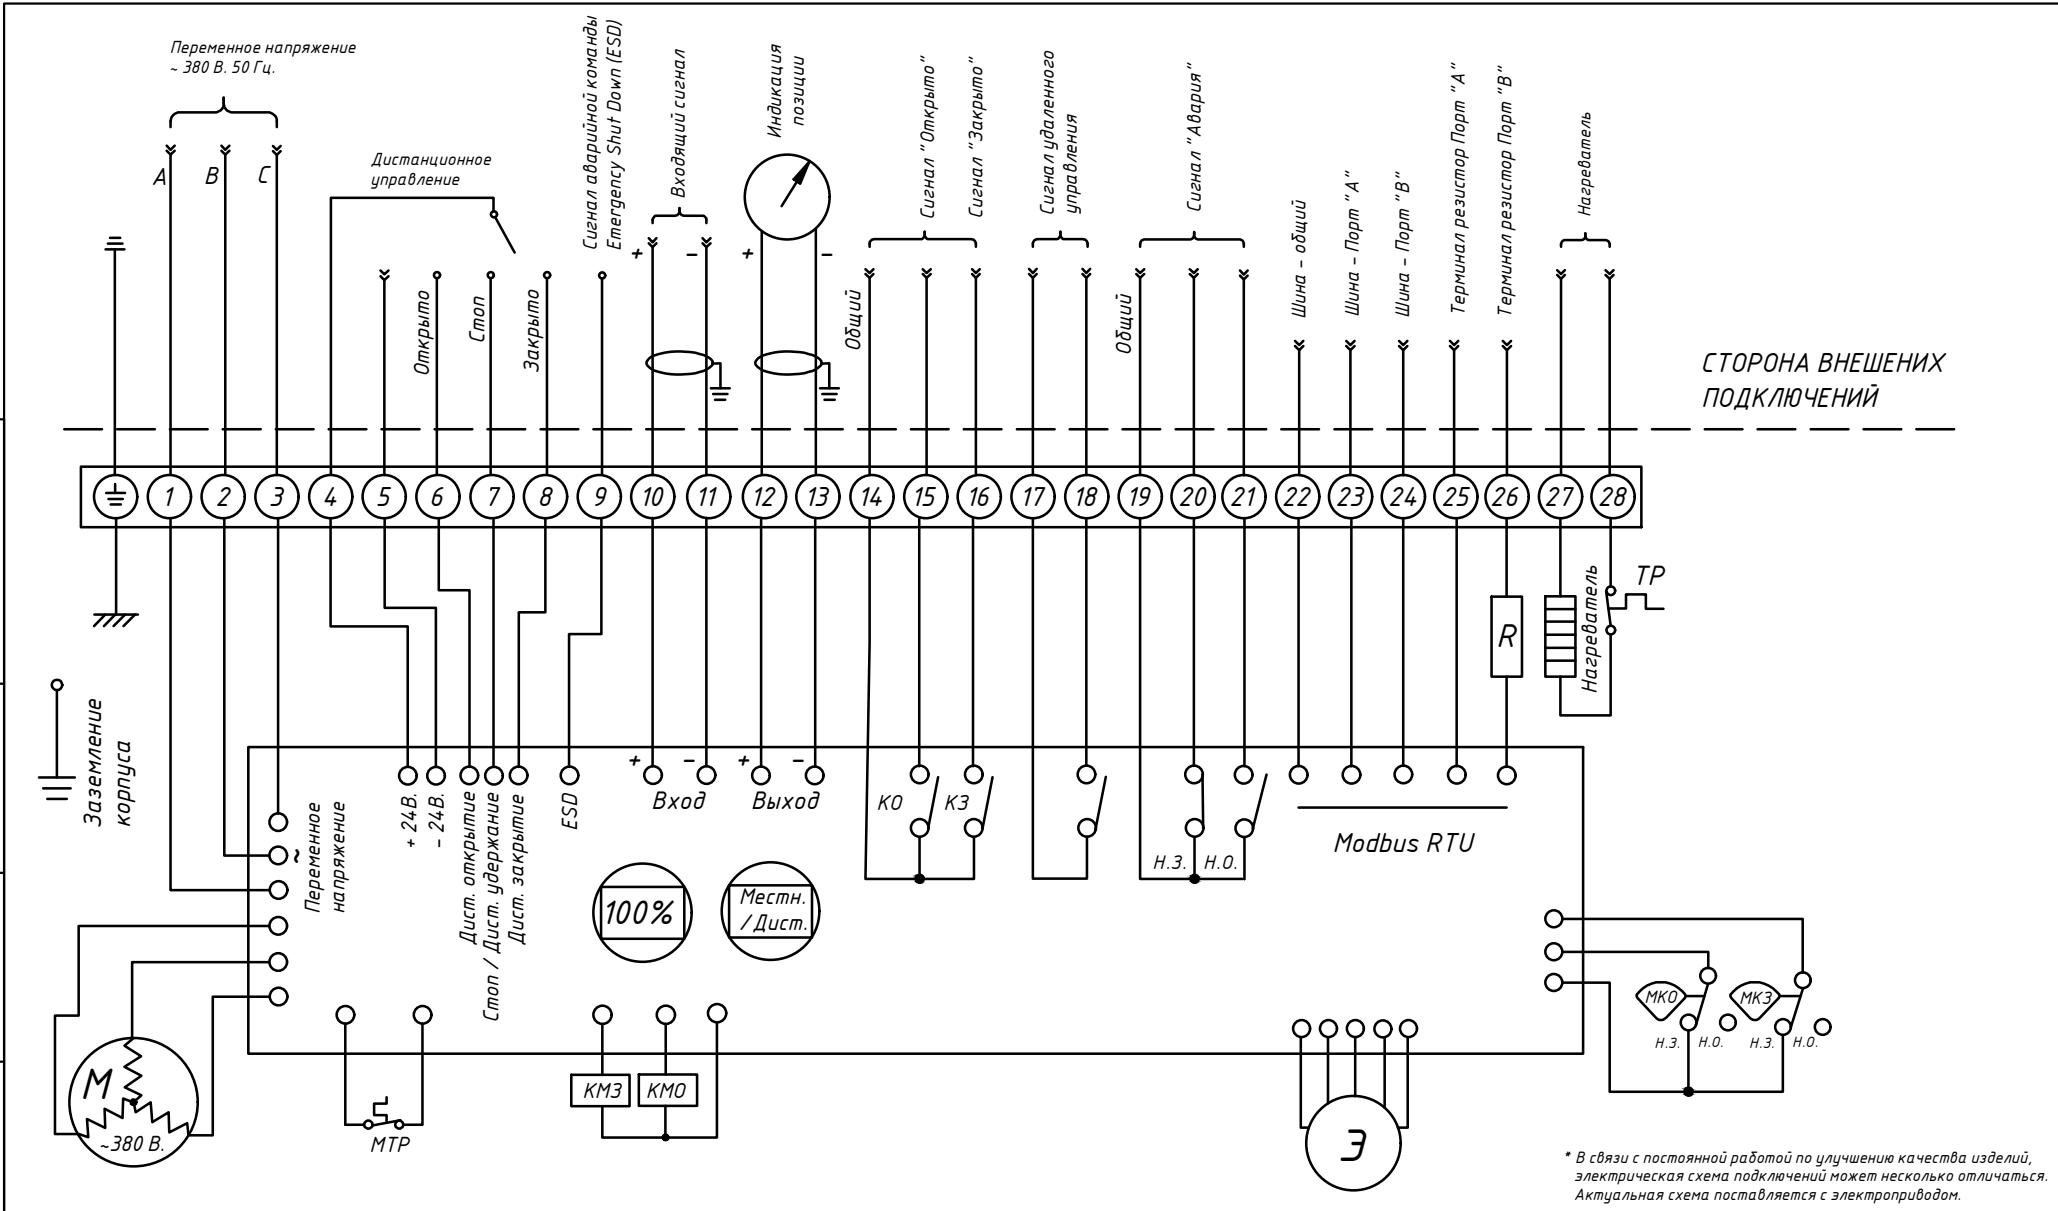

* В связи с постоянной работой по улучшению качества изделий, электрическая схема подключений может несколько отличаться. Актуальная схема поставляется с электроприводом.

ТР - Термо-реле нагревателя
МТР - Термо-реле электродвигателя
М - Электродвигатель
МКЗ, МК0 - Выключатели ограничителя момента
КЗ, К0 - Конечные выключатели
КМЗ, КМ0 - Контакторы
Э - Энкодер

Изм. Лист	№ докум.	Подп.	Дата
Разраб.	Балашов К.В.		05.23
Пров.			
Н.контр.			
Утв.			

AR21E-28F-10		
Электрическая схема электропривода AR21E Напряжение питания: 380В. (переменное). Режим: Интеллектуальный модуль INT/N		
Стадия	Лист	Листов
Р	1	1
Протокол Modbus RTU Модельный ряд: AR21E.007-100		