


Инв. № подл.	Подпись и дата	Взам. инв. №	Инв. № дубл.	Подп. и дата

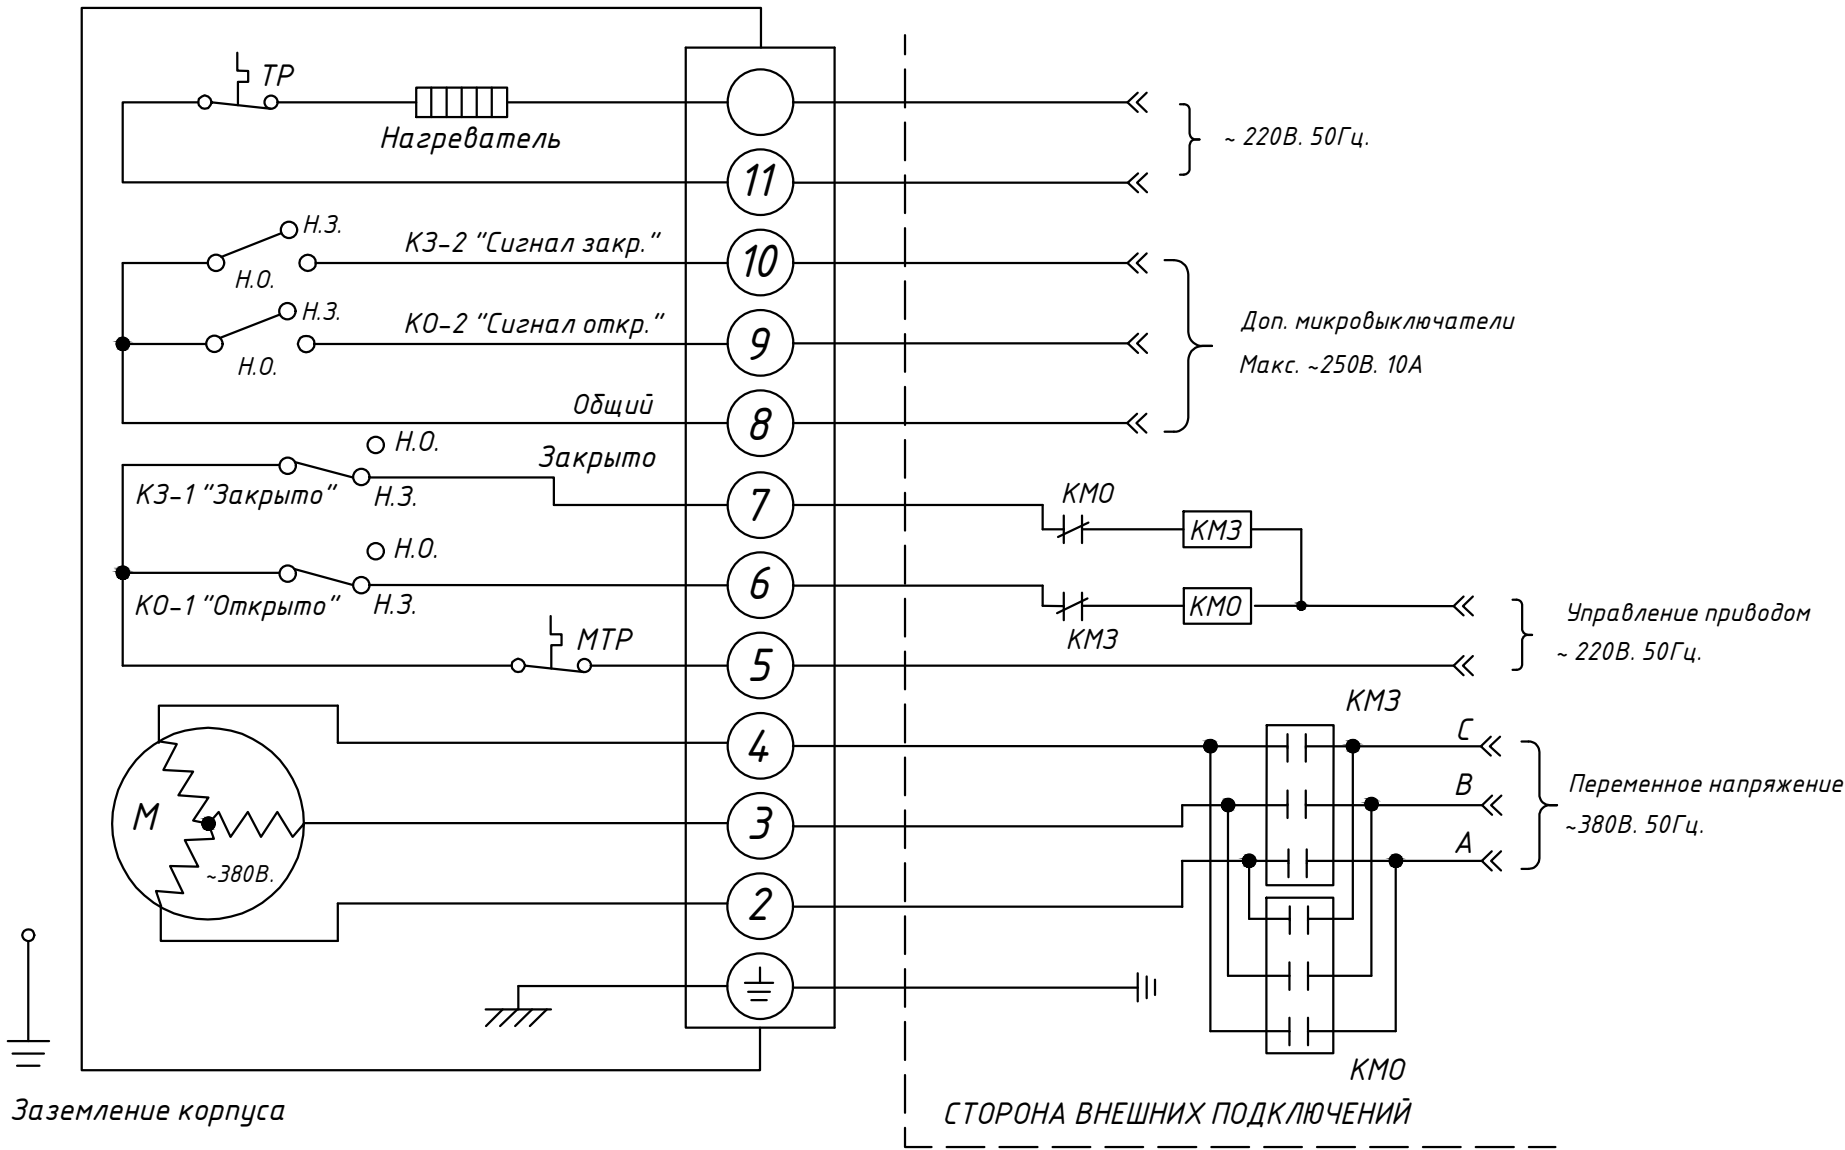

М – Электродвигатель
 МТР – Термо-реле электродвигателя
 ТР – Термореле нагревателя
 КМ0, КМ3 – Контактор
 КЗ – Конечный выключатель положения ЗАКРЫТО
 КО – Конечный выключатель положения ОТКРЫТО

Изм.	Лист	№ докум.	Подп.	Дата
Разраб.				
Пров.				
Н.контр.				
Утв.				

AR01-210H			
Электрическая схема электропривода AR01E	Стадия	Лист	Листов
	Р	1	1
			
Напряжение питания: ~380В. 50 Гц.			
Режим: Закрыто/Открыто			
Модельный ряд: AR01E 005-500			