


Инв. № подл.	Подпись и дата	Взам. инв. №	Инв. № дубл.	Подп. и дата

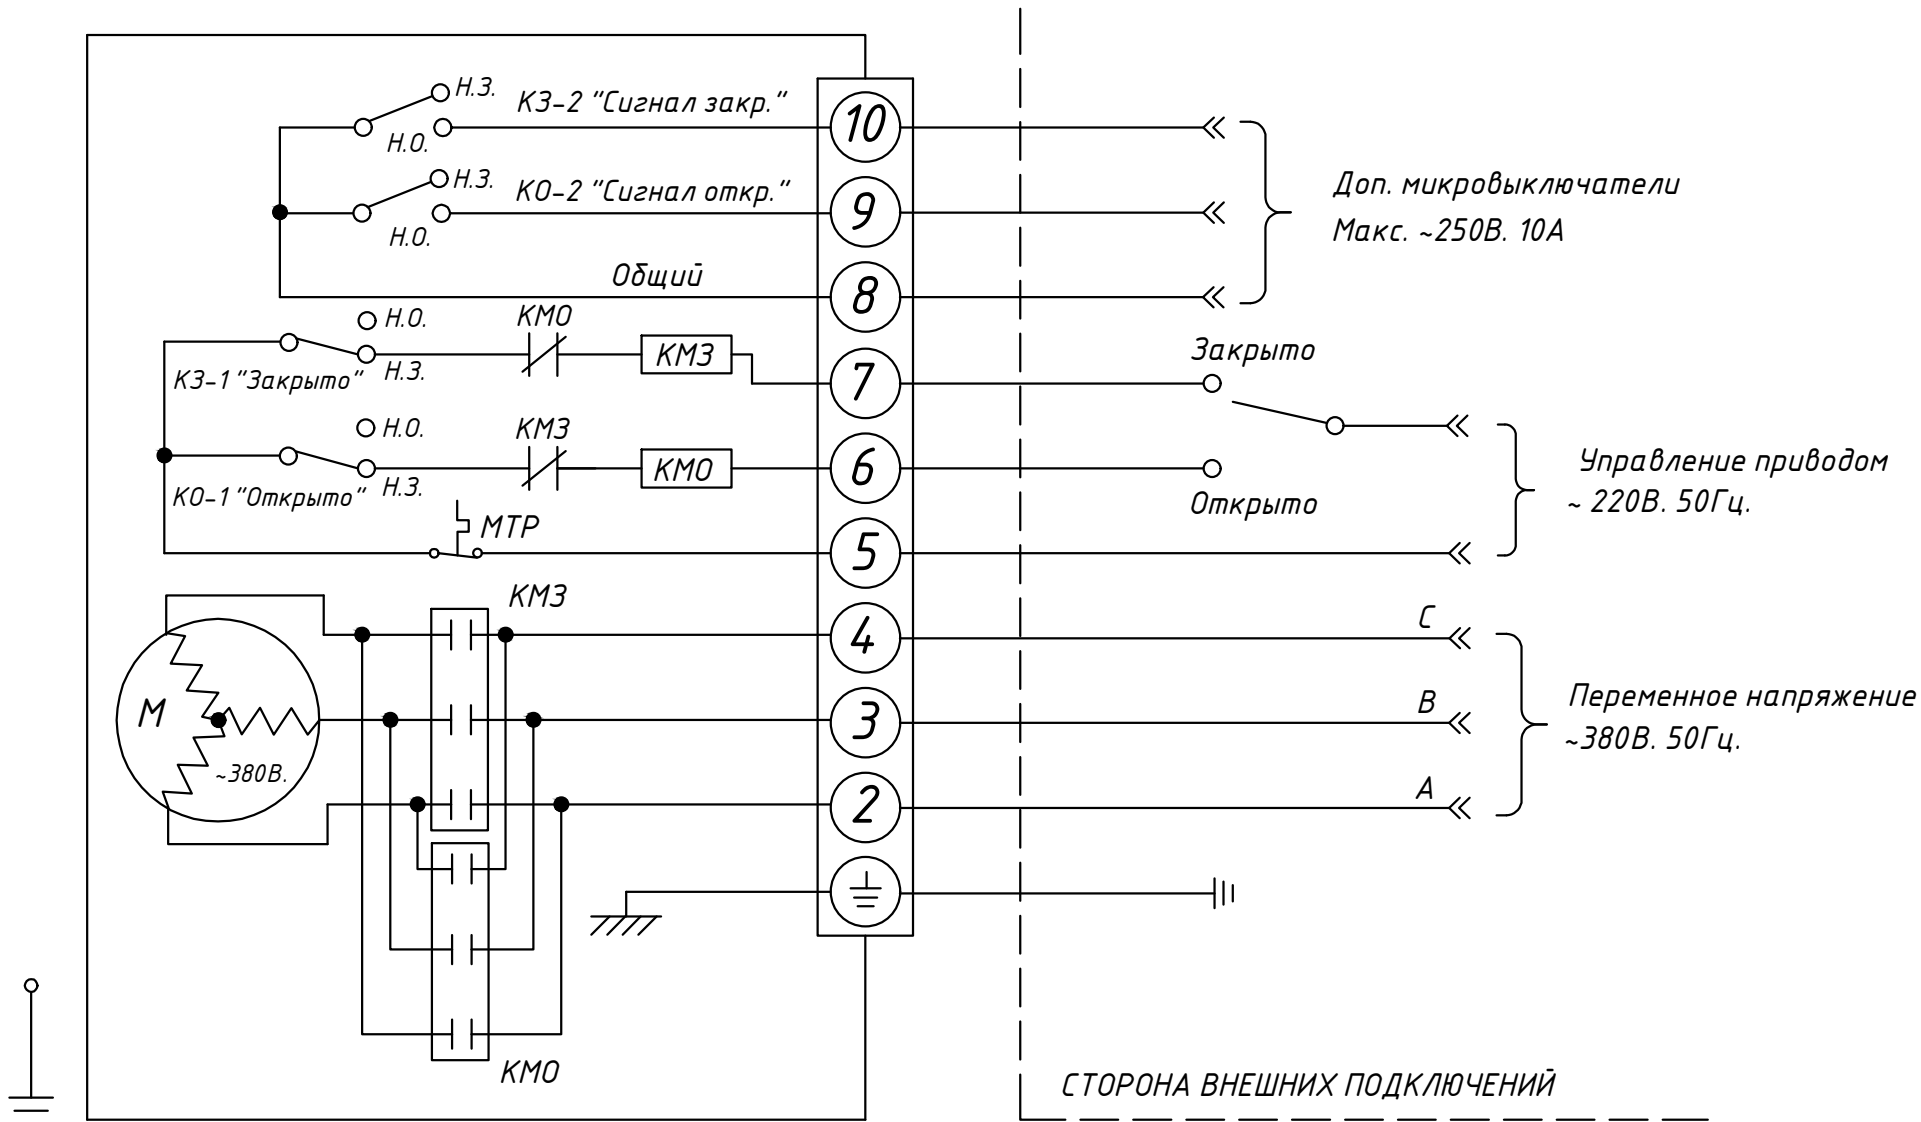

Изм.	Лист	№ докум.	Подп.	Дата
Разраб.				
Пров.				
Н.контр.				
Утв.				

AR01-212

Электрическая схема электропривода AR01E

Напряжение питания: ~380В. 50 Гц.
Режим: Закрыто/Открыто со встроенными
контакторами
Модельный ряд: AR01E 005-500

Стадия	Лист	Листов
Р	1	1



Копировал

Формат А4