


Инв. № подл.	Подпись и дата
Взам. инв. №	Инв. № дубл.
Подпись и дата	

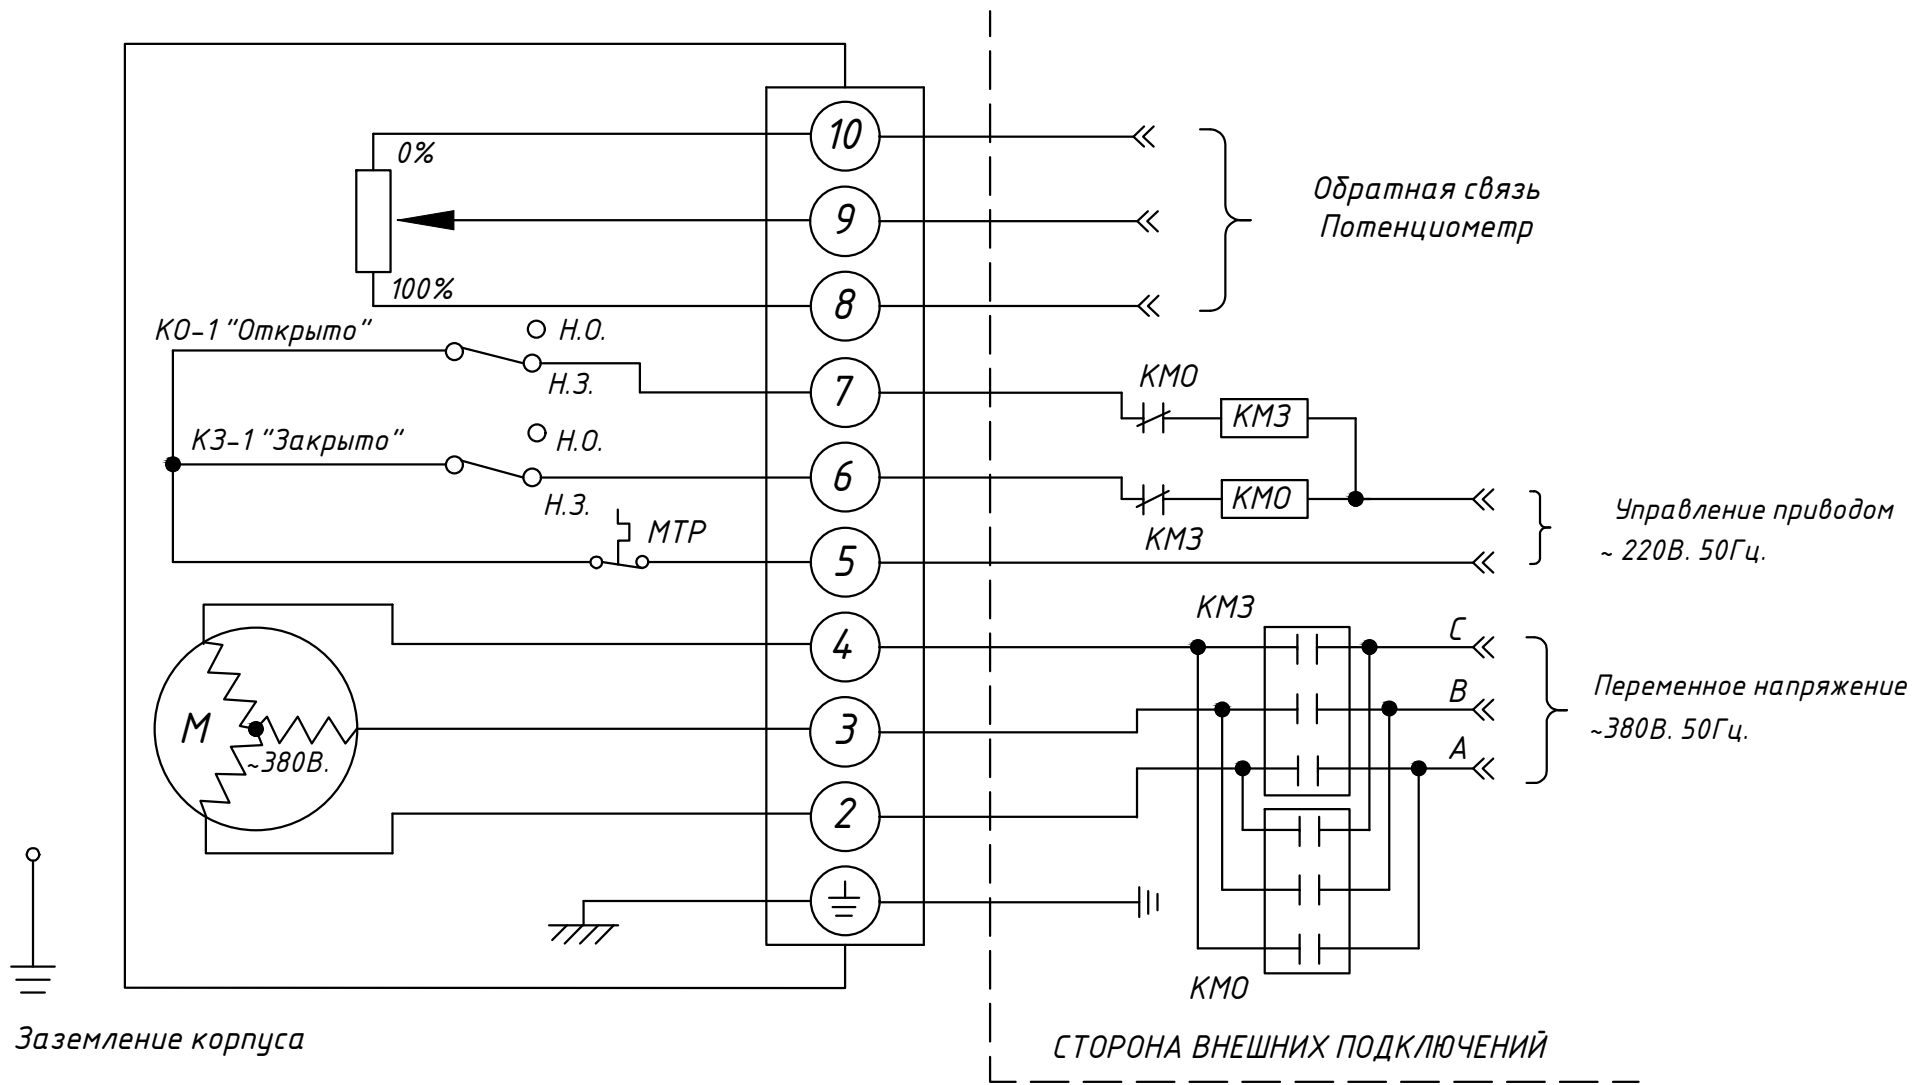

М - Электродвигатель
МТР - Термо-реле электродвигателя
КМО, КМЗ - Контактор
КЗ - Конечный выключатель положения ЗАКРЫТО
КО - Конечный выключатель положения ОТКРЫТО

Изм.	Лист	№ докум.	Подп.	Дата
Разраб.				
Пров.				
Н.контр.				
Утв.				

AR01-260

Электрическая схема электропривода AR01E
Напряжение питания: ~380В. 50 Гц.
Режим: Открыто / Закрыто (Потенциометр)
Модельный ряд: AR01E 005-500

Стадия	Лист	Листов
Р	1	1

