


Инв. № подл.	Подпись и дата	Инв. № дубл.	Подп. и дата
Взам. инв. №			
Подпись и дата			

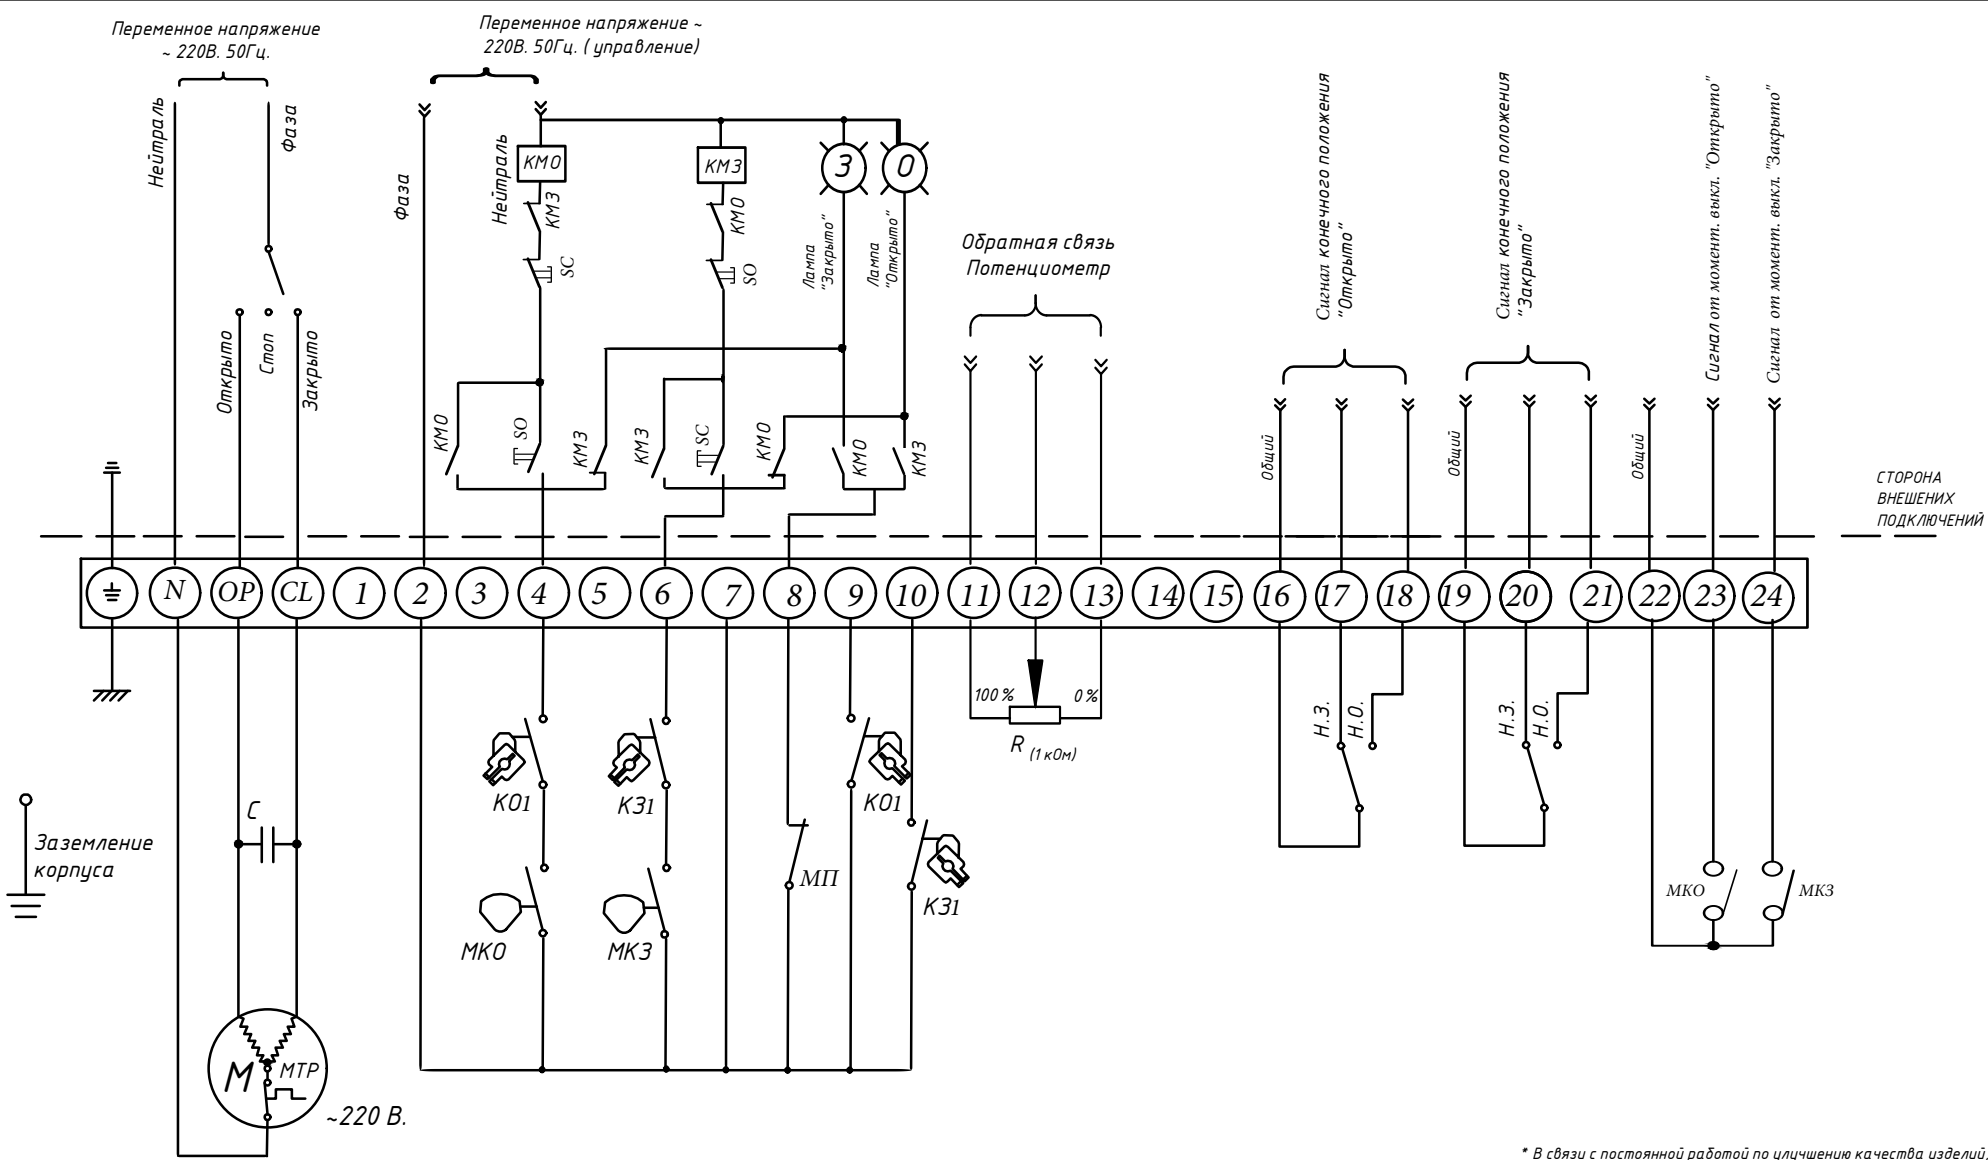

SO, SC – Кнопки управления (Открыть, Закрыть)
 МП – Микровыключатель положения (блинкер)
 М – Электродвигатель
 МКЗ, МКО – Выключатели ограничителя момента
 КЗ, КО – Конечные выключатели
 КМЗ, КМО – Контакторы
 R1 – Потенциометр
 C – Конденсатор

Изм.	Лист	№ докум.	Подп.	Дата
Разраб.				05.23
Пров.				
Н.контр.				
Утв.				

AR19-220-10T

Электрическая схема электропривода AR19E

Напряжение питания: 220В. (переменное).
 Режим: Закрыто / Открыто

Модельный ряд: AR19E

Стадия	Лист	Листов
Р	1	1