


Инв. № подл.	Подпись и дата	Инв. № дубл.	Подп. и дата
Взам. инв. №			
Подпись и дата			

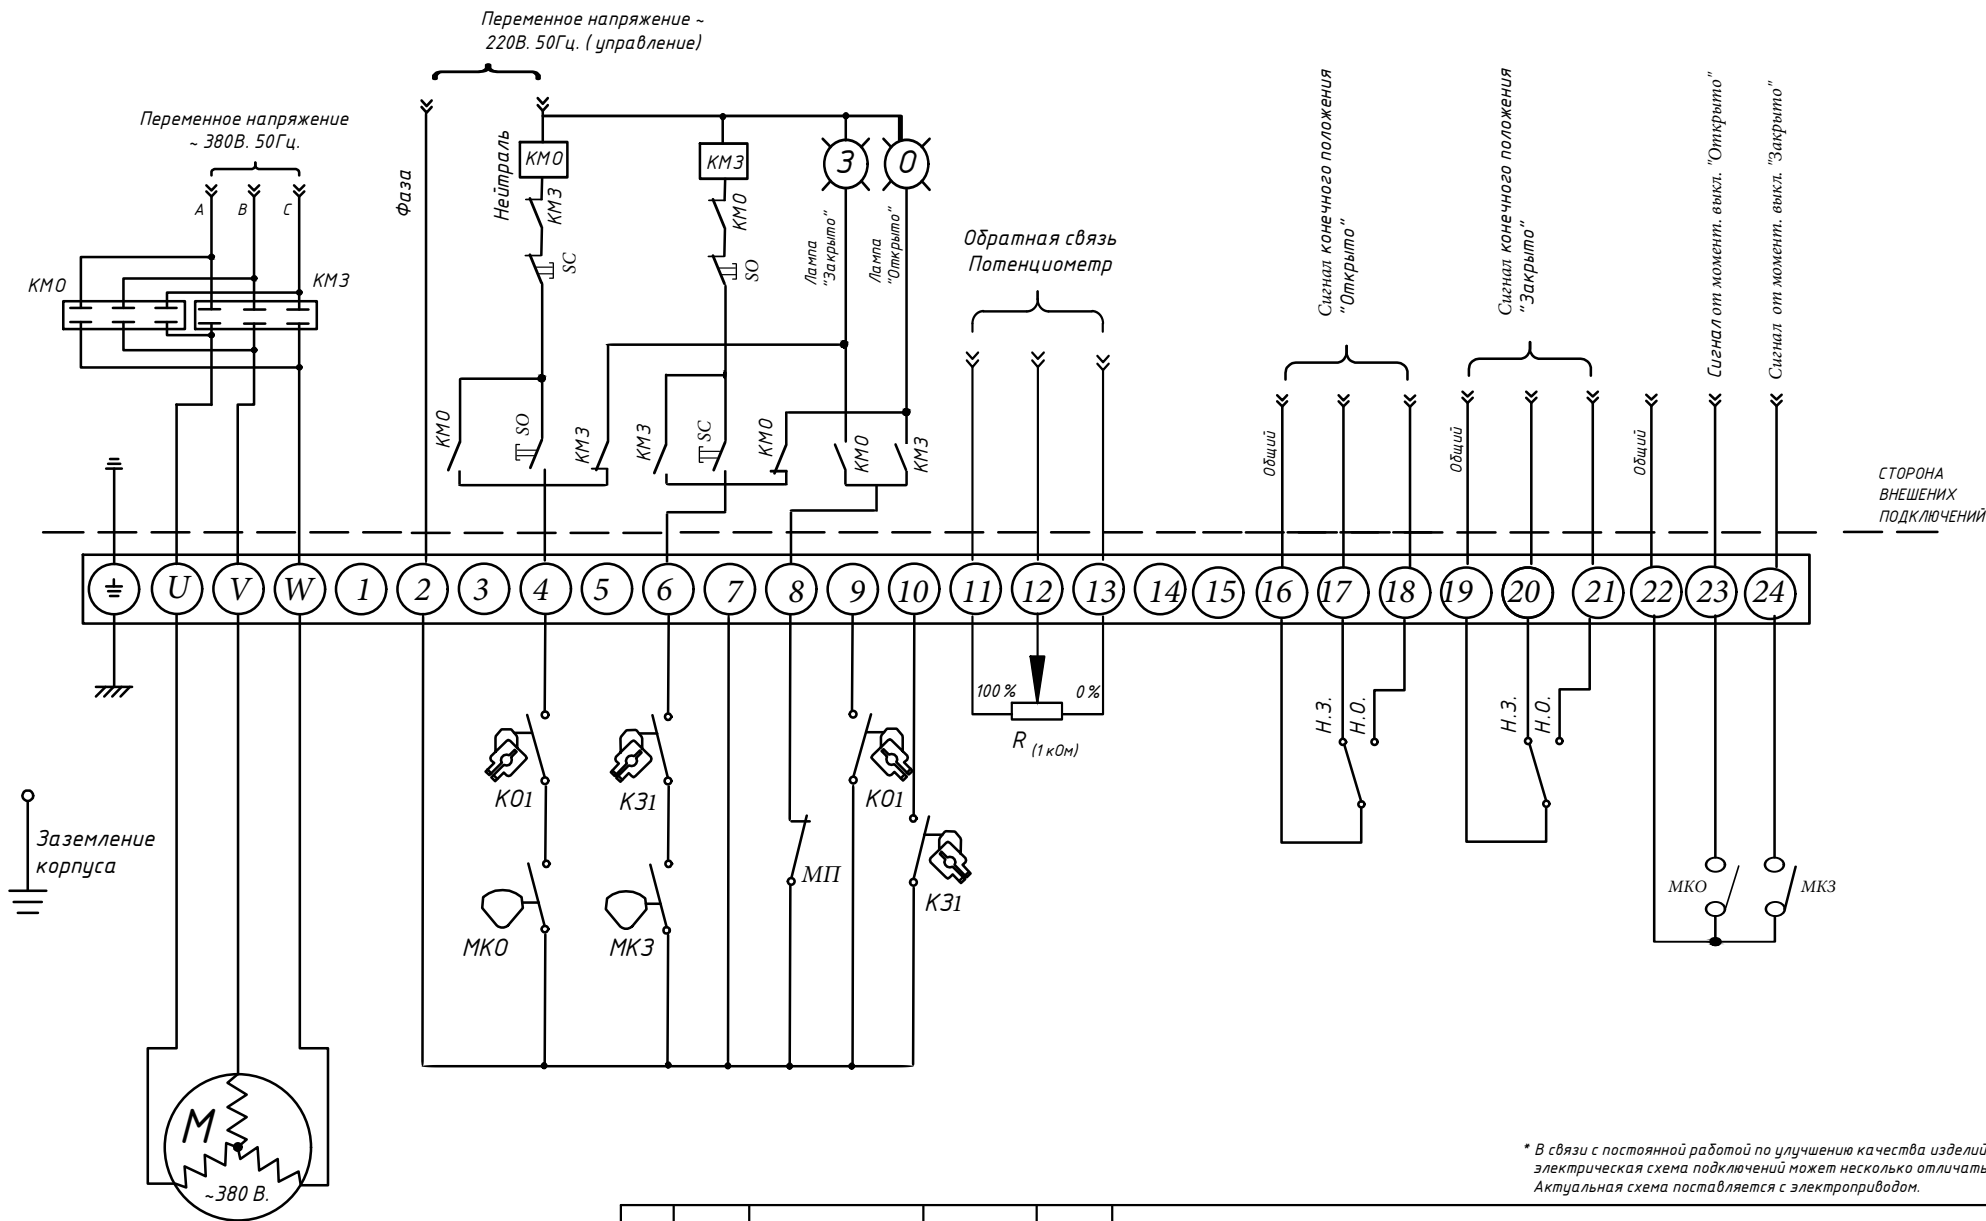

* В связи с постоянной работой по улучшению качества изделий, электрическая схема подключения может несколько отличаться. Актуальная схема поставляется с электроприводом.

AR19-280-10

SO, SC - Кнопки управления (Открыть, Закрыть)
МП - Микровыключатель положения (блинкер)
М - Электродвигатель
МК3, МК0 - Выключатели ограничителя момента
К3, К0 - Конечные выключатели
КМ3, КМ0 - Контакторы
R1 - Потенциометр

Изм.	Лист	№ докум.	Подп.	Дата
Разраб.				05.23
Пров.				
Н.контр.				
Утв.				

Электрическая схема электропривода AR19E

Напряжение питания: 380В. (переменное).
Режим: Закрыто / Открыто

Модельный ряд: AR19E

Стадия	Лист	Листов
P	1	1

Формат А4