


Инв. № подл.	Подпись и дата	Инв. № дубл.	Подп. и дата
Взам. инв. №			
Подпись и дата			

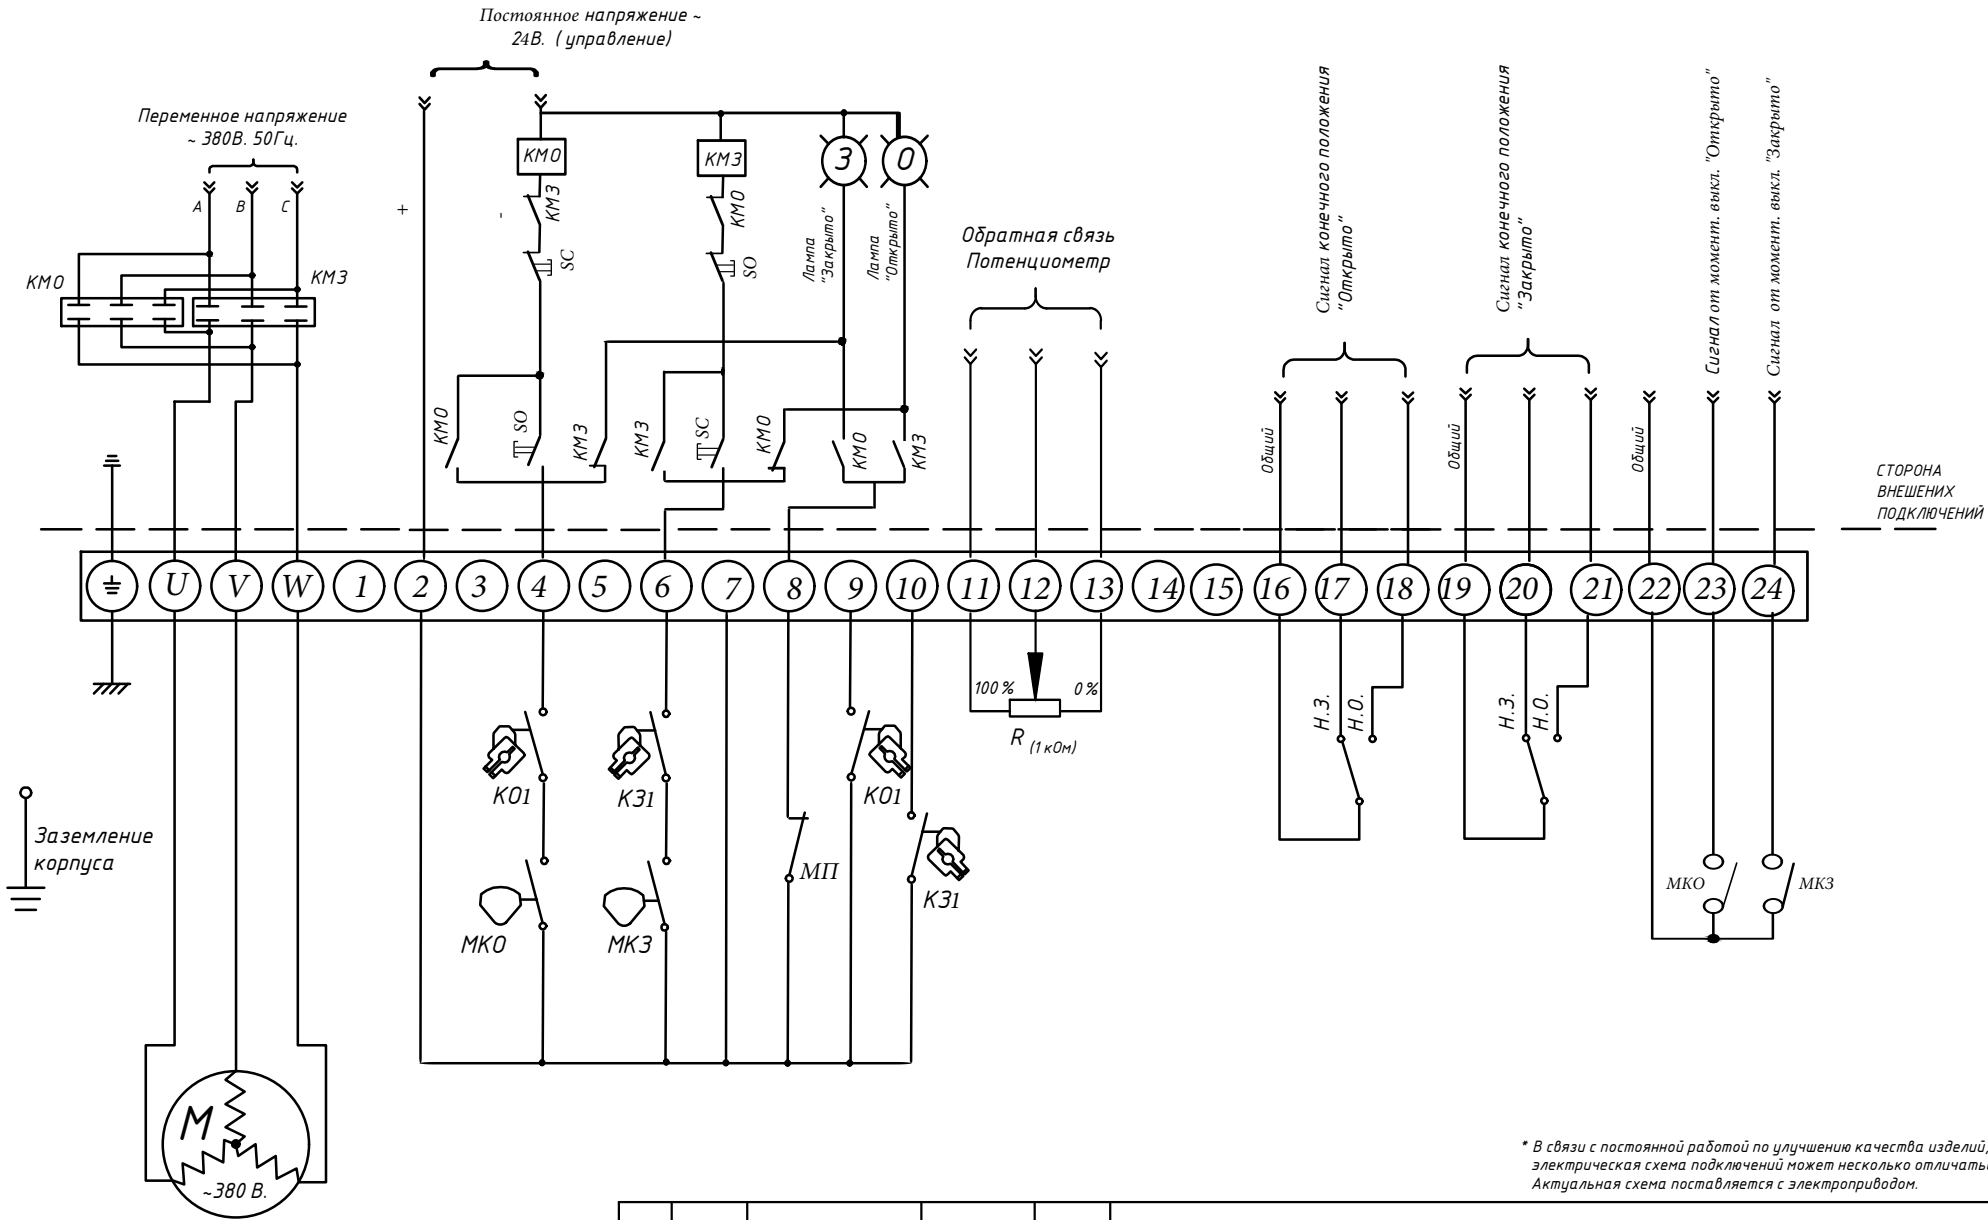

* В связи с постоянной работой по улучшению качества изделий, электрическая схема подключений может несколько отличаться. Актуальная схема поставляется с электроприводом.

SO, SC - Кнопки управления (Открыть, Закрыть)
 МП - Микровыключатель положения (блинкер)
 М - Электродвигатель
 МКЗ, МКО - Выключатели ограничителя момента
 КЗ, К0 - Конечные выключатели
 КМЗ, КМ0 - Контакторы
 R1 - Потенциометр

Изм.	Лист	№ докум.	Подп.	Дата
Разраб.				05.23
Пров.				
Н.контр.				
Утв.				

AR19-280-10		
Электрическая схема электропривода AR19E		
Напряжение питания: 380В. (переменное). Режим: Закрыто / Открыто		
Модельный ряд: AR19E		
Стадия	Лист	Листов
P	1	1