


Инв. № подл.	Подпись и дата	Инв. № дубл.	Взам. инв. №

Напряжение питания однофазное, переменное ~ 220В. 50Гц

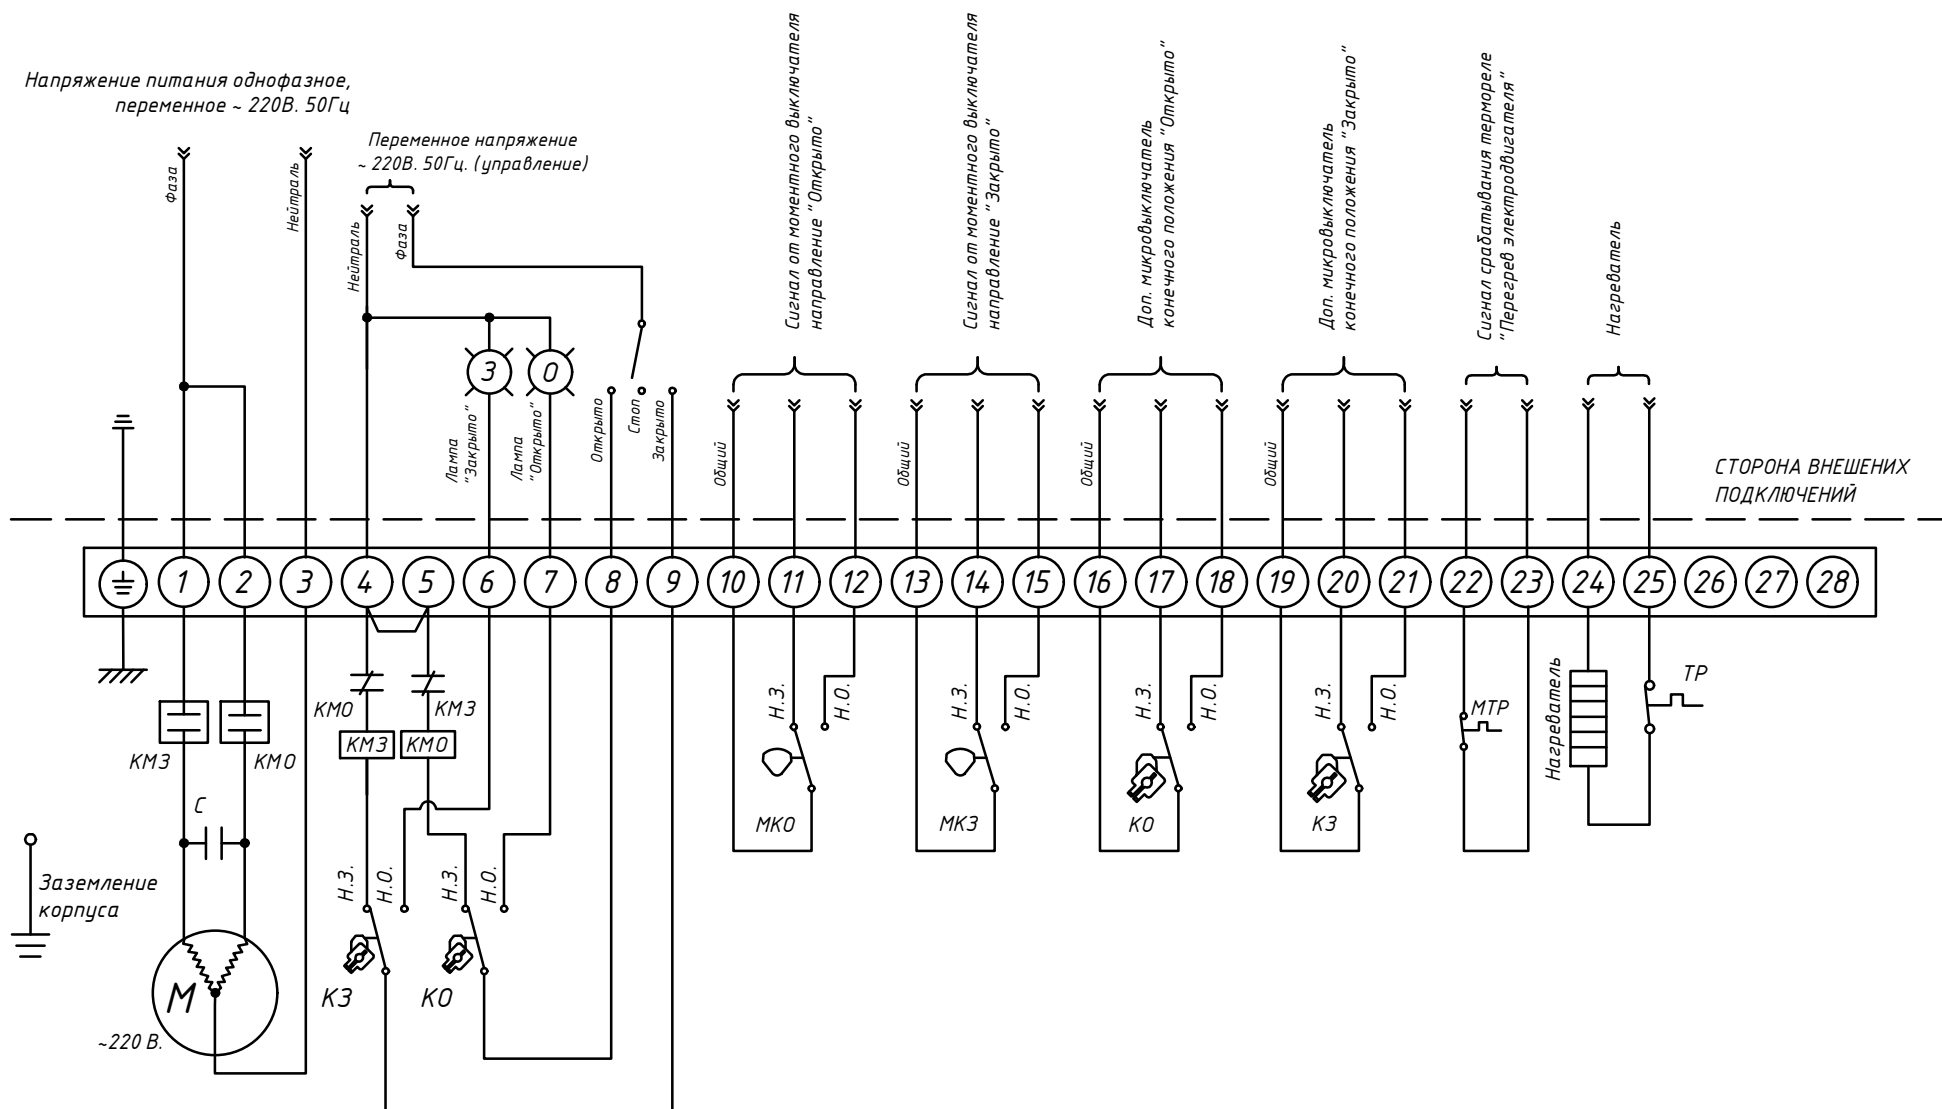

ТР - Термо-реле нагревателя
 МТР - Термо-реле электродвигателя
 М - Электродвигатель
 МКЗ, МКО - Выключатели ограничителя момента
 КЗ, КО - Конечные выключатели
 КМЗ, КМО - Контакторы
 С - Конденсатор

Изм.	Лист	№ докум.	Подп.	Дата
Разраб.	Балашов К.В.			05.23
Пров.				
Н.контр.				
Утв.				

AR21E-110-10

Электрическая схема электропривода AR21E		
Стадия	Лист	Листов
Р	1	1

Напряжение питания: ~220В. 50 Гц.
 Режим: Закрыто/Открыто

Модельный ряд: AR21E.007-100

* В связи с постоянной работой по улучшению качества изделий, электрическая схема подключений может несколько отличаться. Актуальная схема поставляется с электроприводом.