


Инв. № подл.	Подпись и дата	Взам. инв. №	Инв. № дубл.	Подп. и дата

Напряжение питания однофазное,
переменное ~ 220В. 50Гц

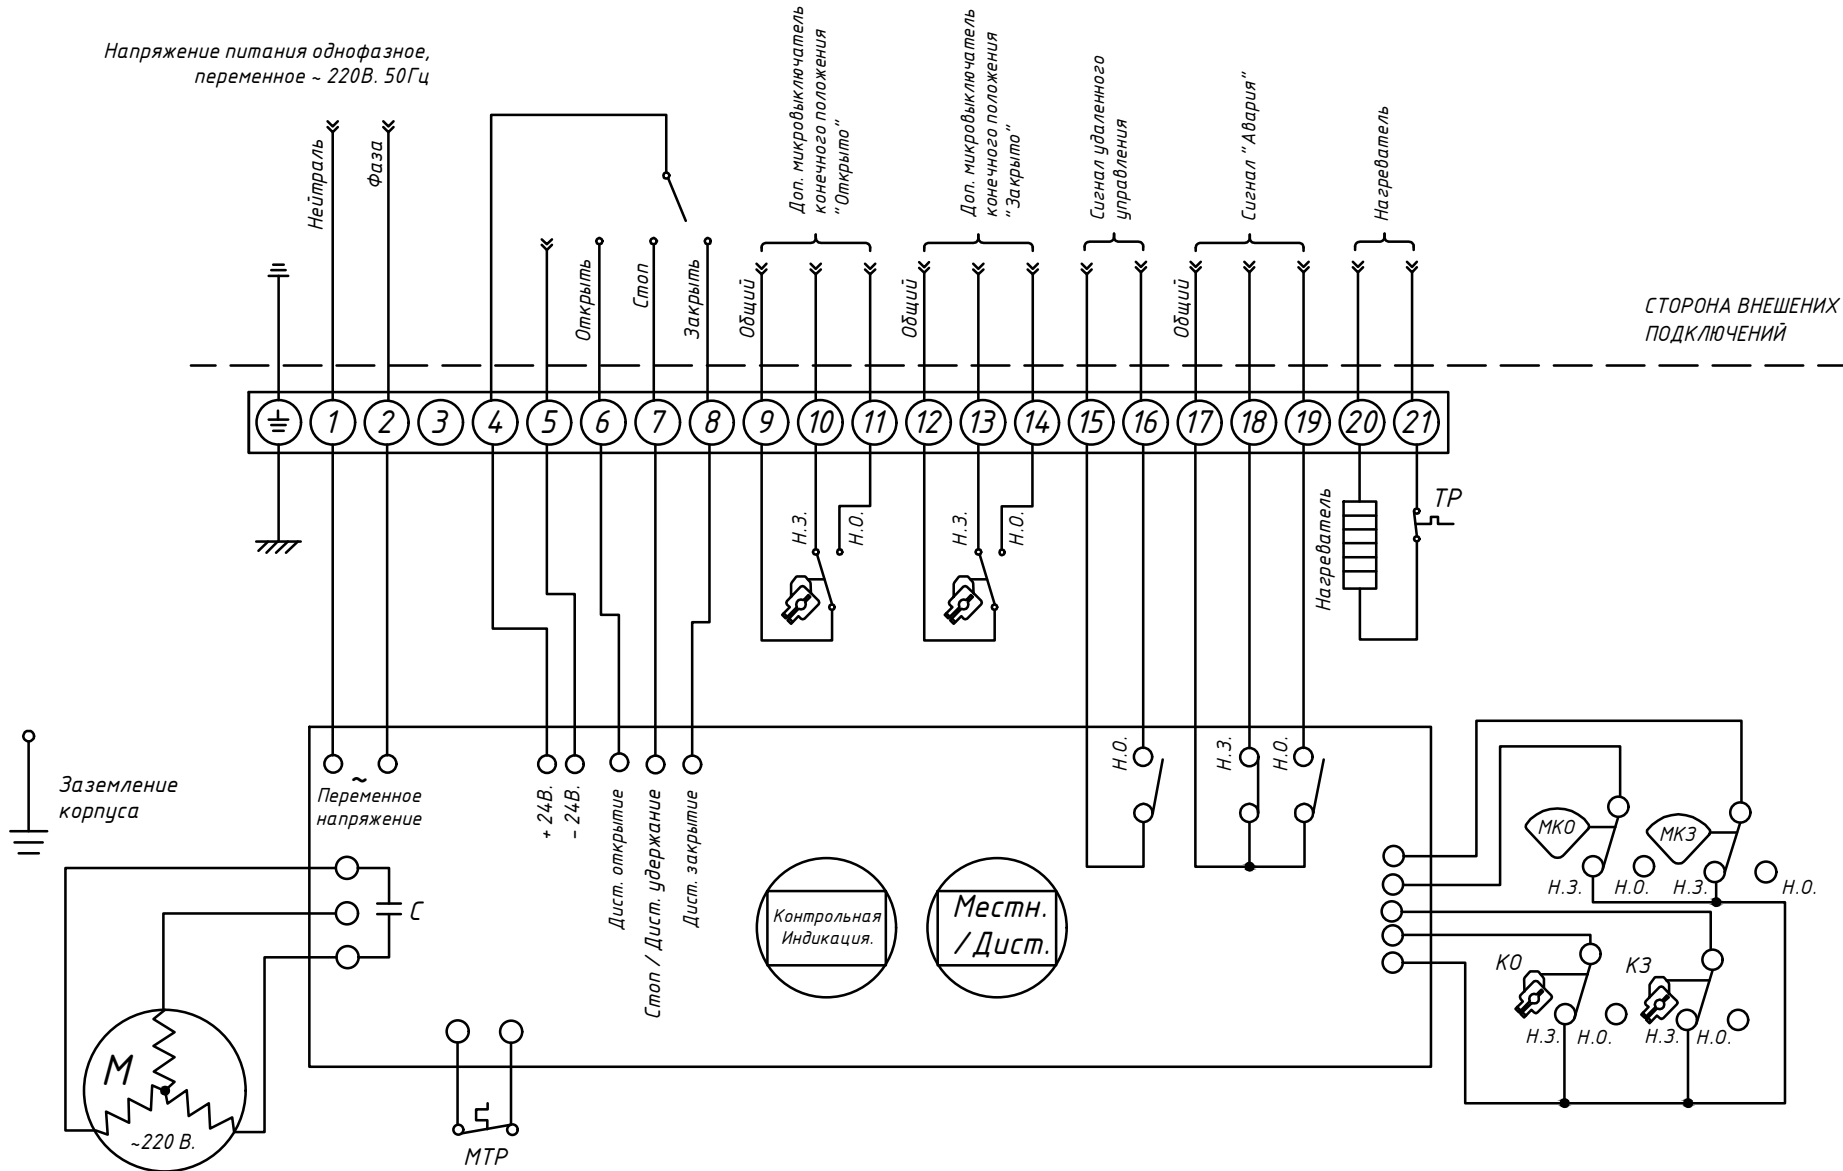

ТР - Термо-реле нагревателя
МТР - Термо-реле электродвигателя
М - Электродвигатель
МКЗ, МКО - Выключатели ограничителя момента
КЗ, КО - Конечные выключатели
С - Конденсатор

Изм.	Лист	№ докум.	Подп.	Дата
Разраб.	Балашов К.В.			05.23
Пров.				
Н.контр.				
Утв.				

AR21-131-10

Электрическая схема электропривода AR21E
Напряжение питания: 220В. (переменное).
Режим: Интеллектуальный модуль INT/O
Модельный ряд: AR21E.007-050

Стадия	Лист	Листов
Р	1	1