


Напряжение питания однофазное,
переменное ~ 220В. 50Гц

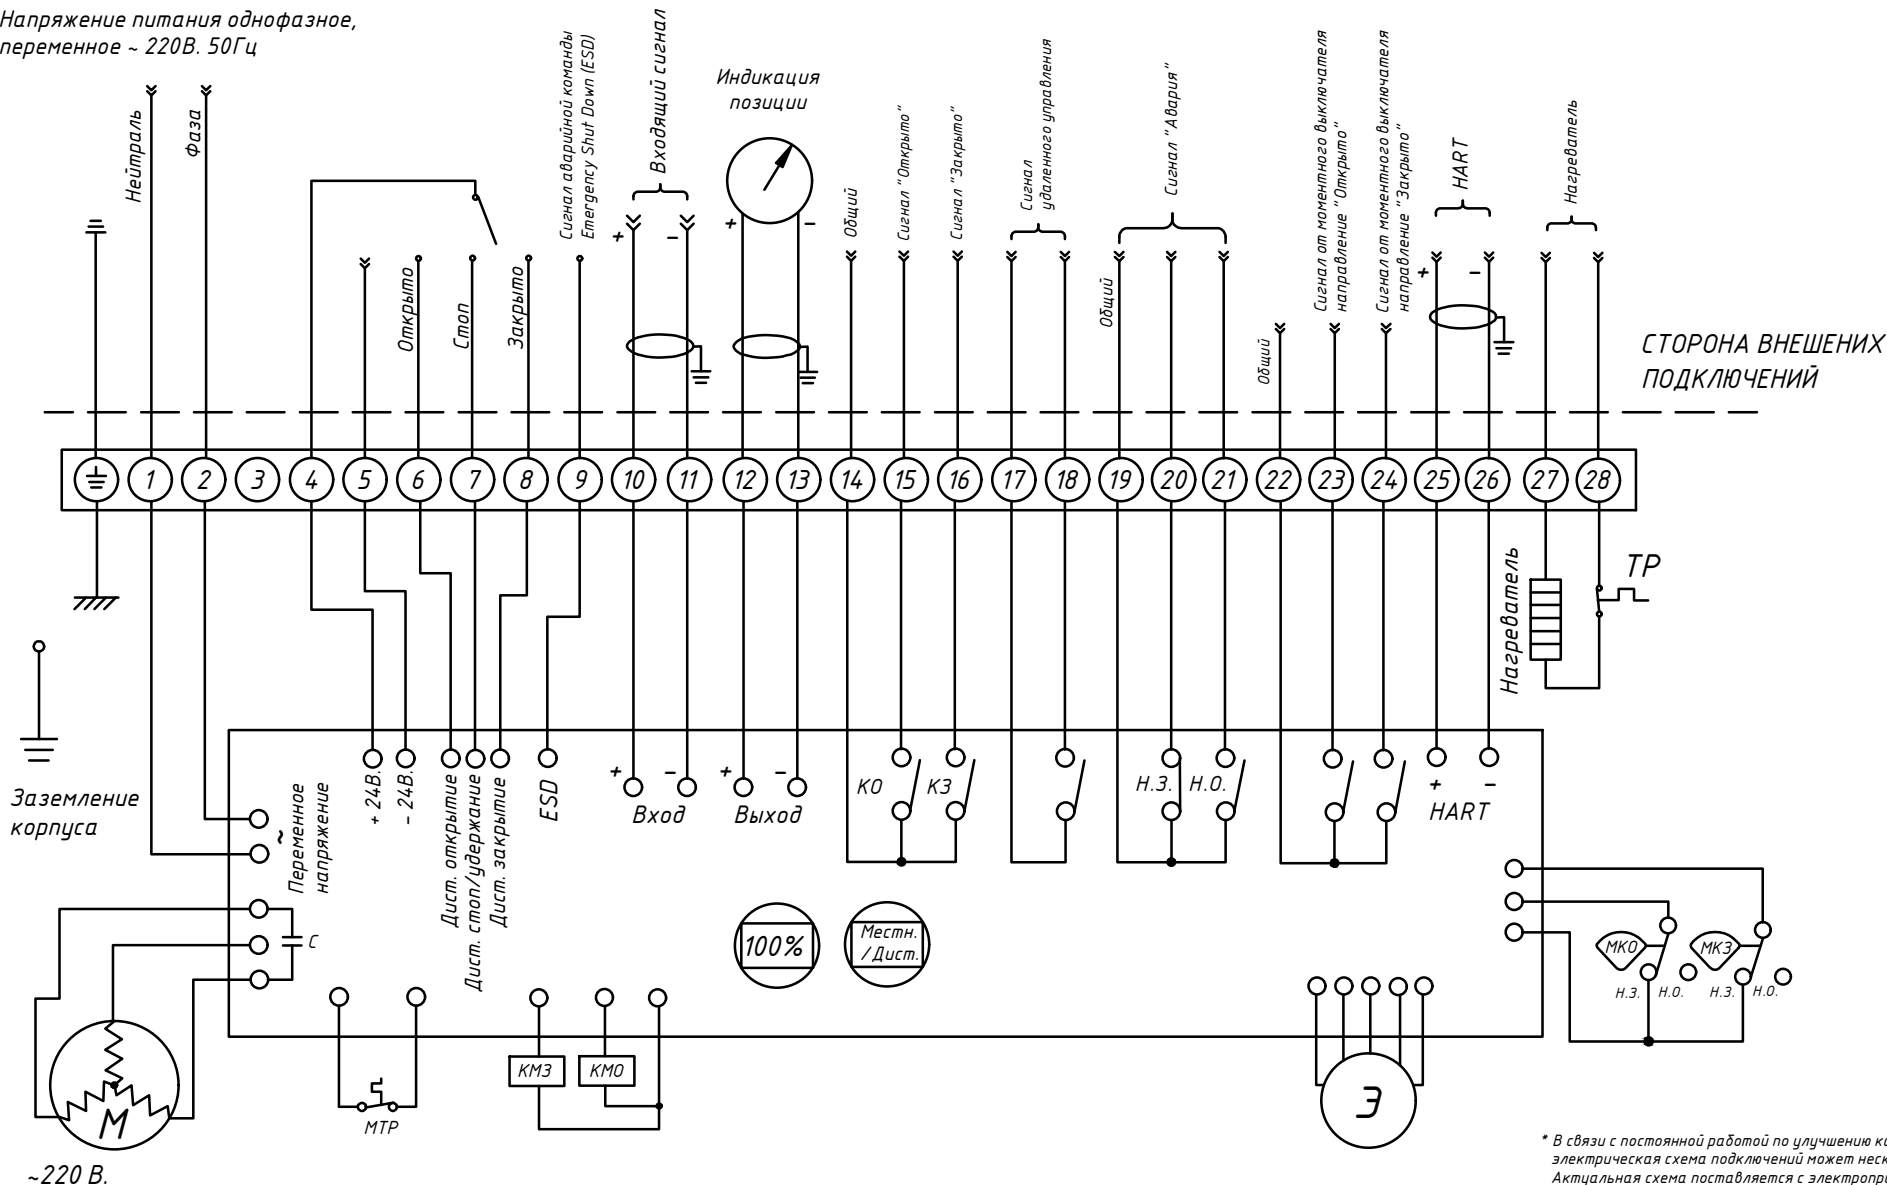

~220 В.

ТР - Термо-реле нагревателя

Э - Энкодер

М - Электродвигатель

МТР - Термо-реле электродвигателя

КМЗ, КМО - Контакторы

КЗ, КО - Конечные выключатели

МКЗ, МКО - Выключатели ограничителя момента

С - Конденсатор

* В связи с постоянной работой по улучшению качества изделий,
электрическая схема подключений может несколько отличаться.
Актуальная схема поставляется с электроприводом.

AR21E-18C-10

Изм.	Лист	№ докум.	Подп.	Дата
Разраб.	Балашов К.В.			05.23
Пров.				
Н.контр.				
Утв.				

Электрическая схема электропривода AR21E
Напряжение питания: 220В. (переменное).
Режим: Интеллектуальный модуль INT/N

Протокол HART
Модельный ряд: AR21E.007-100

Стадия	Лист	Листов
Р	1	1



Копировал

Формат А4