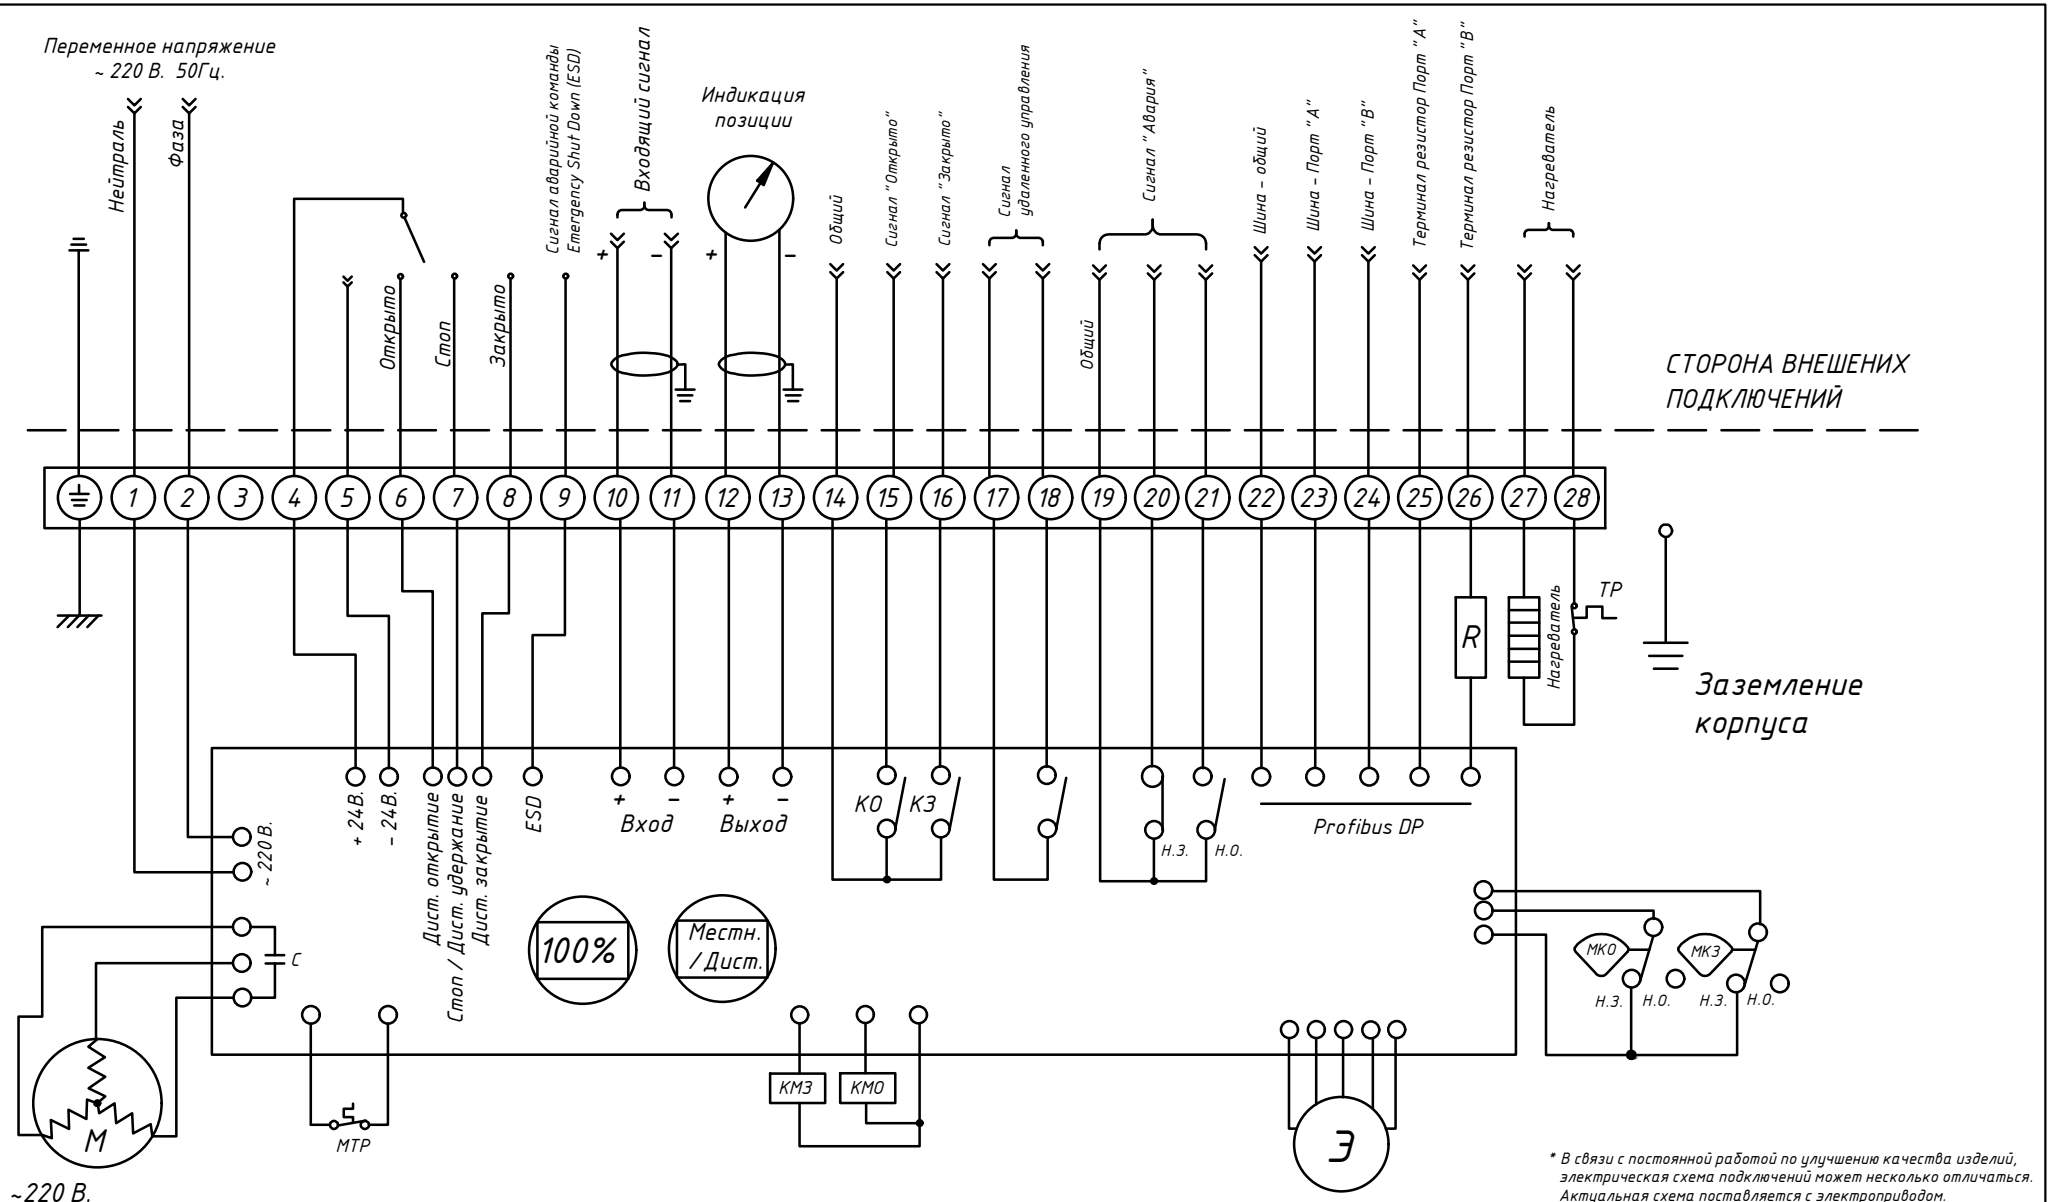

~220 В.

ТР – Термо-реле нагревателя
Э – Энкодер
М – Электродвигатель
МТР – Термо-реле электродвигателя
КМЗ, КМО – Контакторы
КЗ, КО – Конечные выключатели
МКЗ, МКО – Выключатели ограничителя момента
С – Конденсатор

* В связи с постоянной работой по улучшению качества изделий, электрическая схема подключений может несколько отличаться. Актуальная схема поставляется с электроприводом.

Изм.	Лист	№ докум.	Подп.	Дата
Разраб.		Балашов К.В.		05.23
Пров.				
Н.контр.				
Утв.				

AR21E-18F-10

Электрическая схема электропривода AR21E
Напряжение питания: 220В. (переменное).
Режим: Интеллектуальный модуль INT/N

Протокол Profibus DP
Модельный ряд: AR21E.007-100

Стадия	Лист	Листов
Р	1	1

АРХИМЕД

Подп. и дата | Инв. № дубл. | Взам. инв. № | Подпись и дата | Инв. № подл.

Копировал

Формат А4