


Инв. № подл.	Взам. инв. №	Инв. № дубл.	Подп. и дата
Инв. № подл.	Взам. инв. №	Инв. № дубл.	Подп. и дата

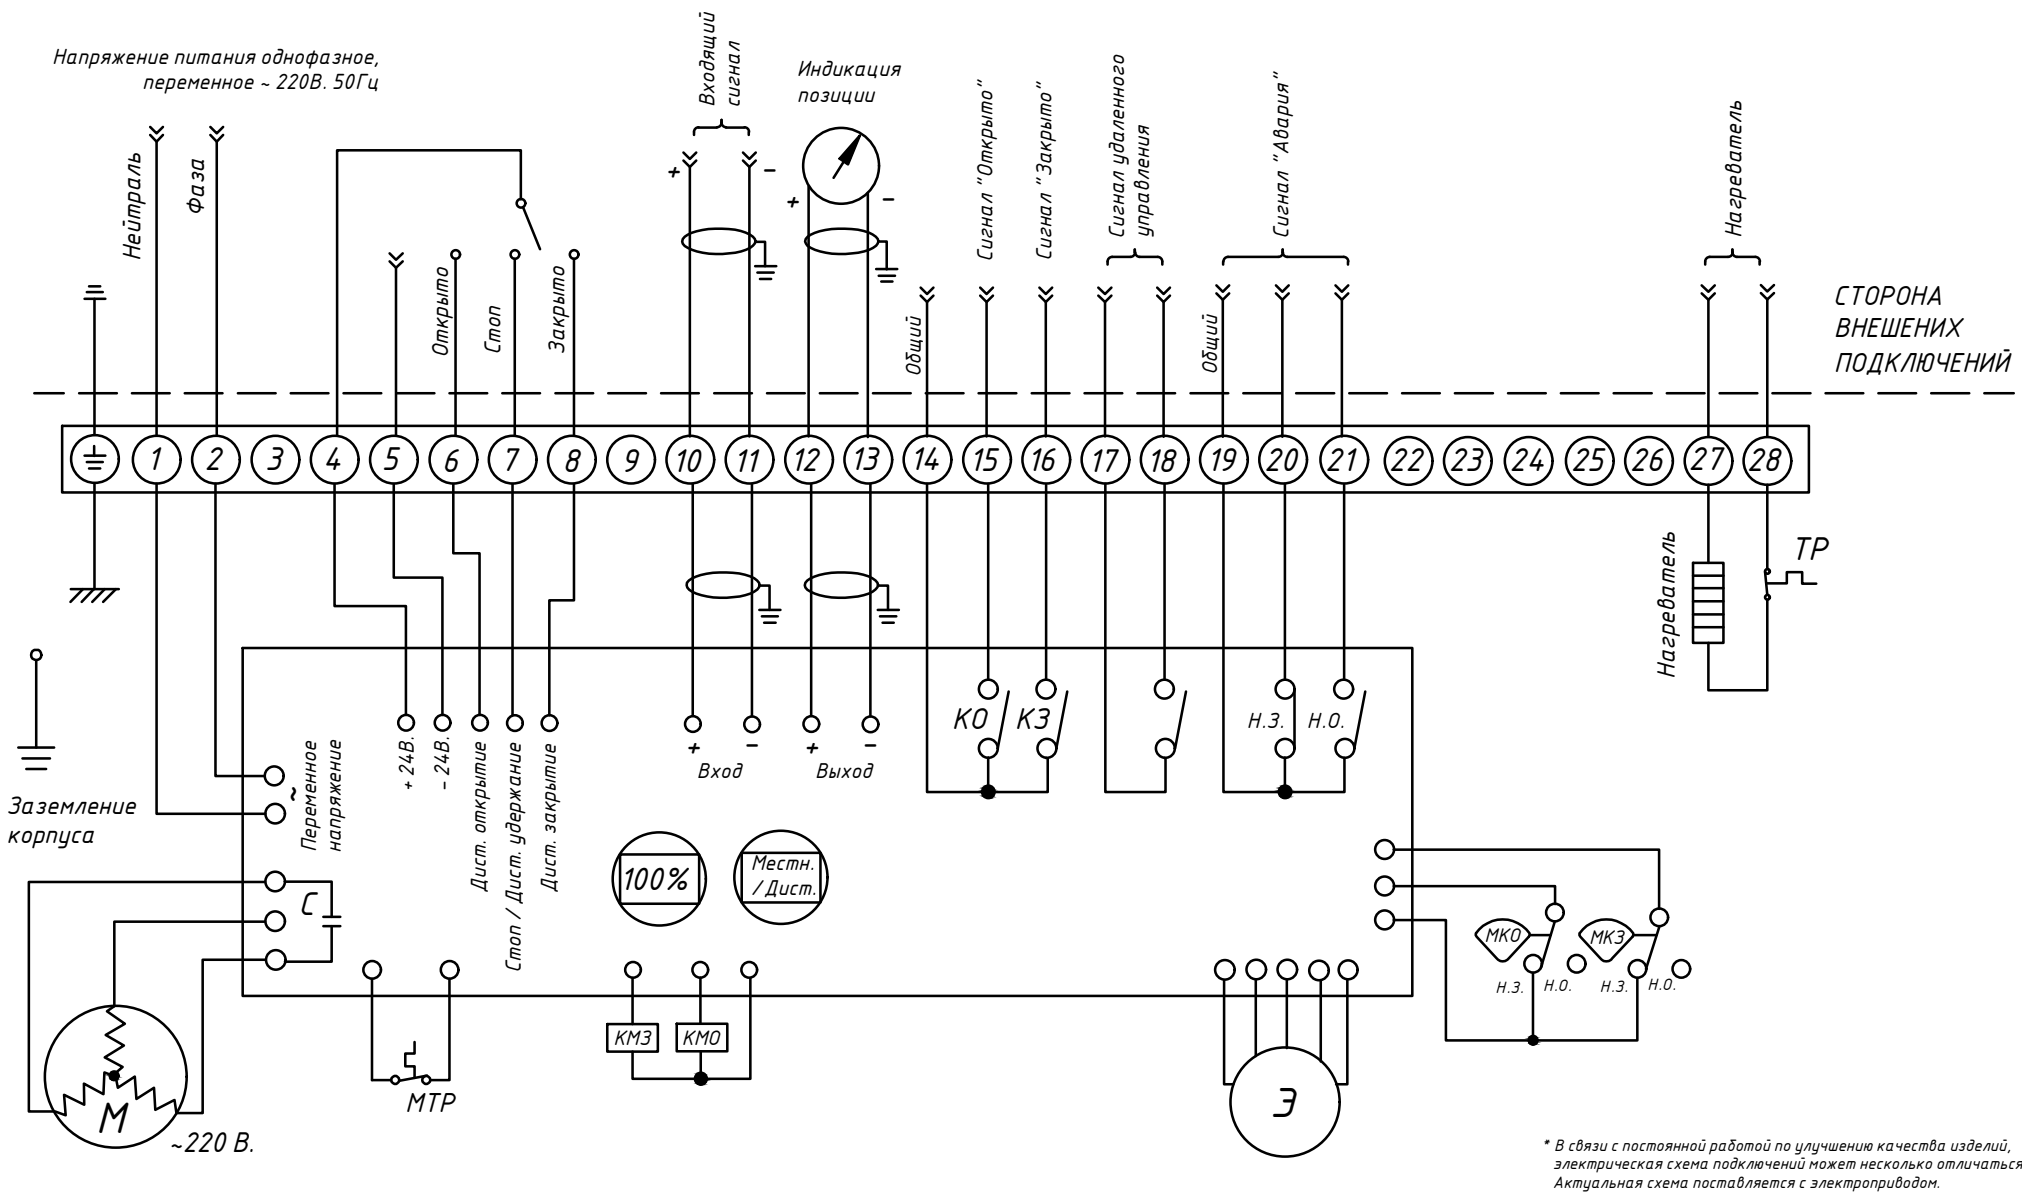

ТР - Термо-реле нагревателя
 Э - Энкодер
 М - Электродвигатель
 МТР - Термо-реле электродвигателя
 КМЗ, КМО - Контакторы
 КЗ, КО - Конечные выключатели
 МКЗ, МКО - Выключатели ограничителя момента
 С - Конденсатор

Изм. Лист	№ докум.	Подп.	Дата
Разраб.	Балашов К.В.		05.23
Пров.			
Н.контр.			
Утв.			

AR21E-1A7-10

Электрическая схема электропривода AR21E

Напряжение питания: ~220В. 50 Гц.
 Режим: Интеллектуальный модуль INT/L

Модельный ряд: AR21E.007-100

Стадия	Лист	Листов
Р	1	1

* В связи с постоянной работой по улучшению качества изделий, электрическая схема подключений может несколько отличаться. Актуальная схема поставляется с электроприводом.