


Инв. № подл.	Подпись и дата	Взам. инв. №	Инв. № дубл.	Подп. и дата

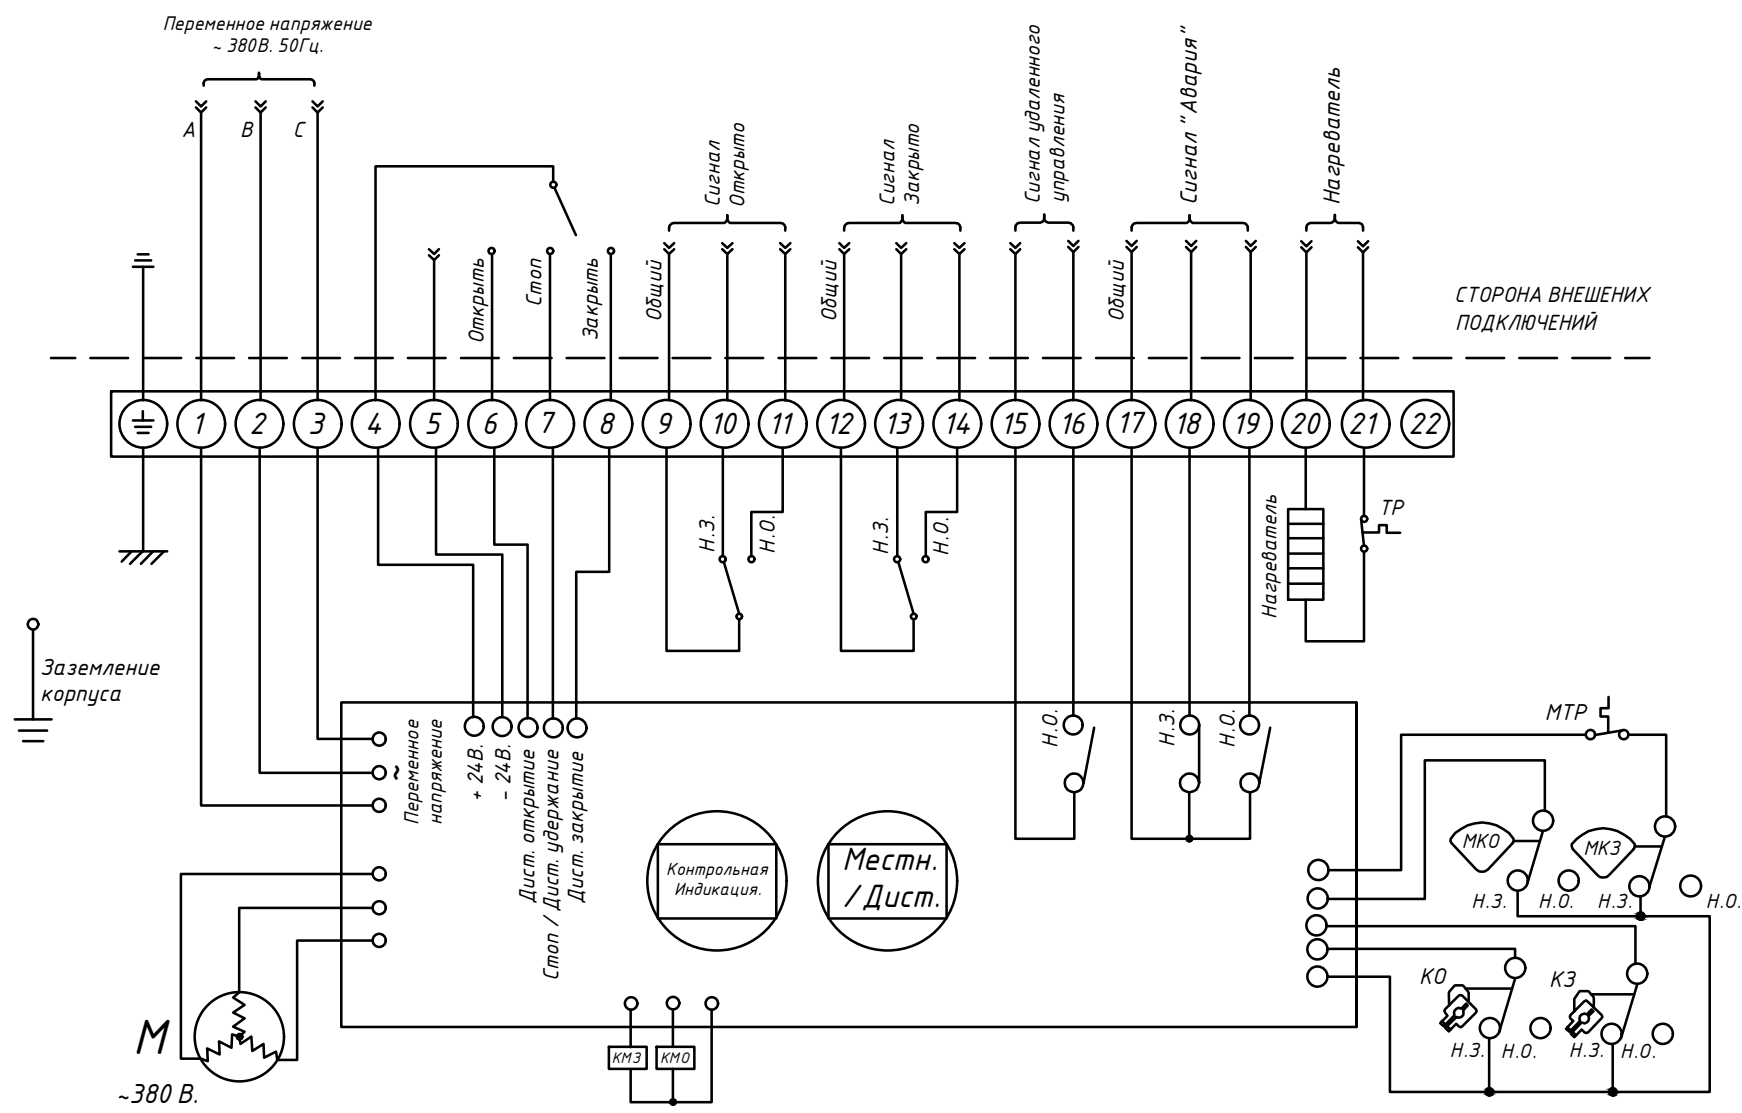

ТР - Термо-реле нагревателя
 МТР - Термо-реле электродвигателя
 М - Электродвигатель
 МКЗ, МКО - Выключатели ограничителя момента
 КЗ, КО - Конечные выключатели
 КМЗ, КМО - Контакторы

Изм.	Лист	№ докум.	Подп.	Дата
Разраб.	Балашов К.В.			05.23
Пров.				
Н.контр.				
Утв.				

AR21E-231-10

Электрическая схема электропривода AR21E Напряжение питания: 380В. (переменное).	Стадия	Лист	Листов
	Р	1	1

Режим: Интеллектуальный модуль INT/O
 Модельный ряд: AR11E21.007-100