


Инв. № подл.	Подпись и дата	Взам. инв. №	Инв. № дубл.	Подп. и дата

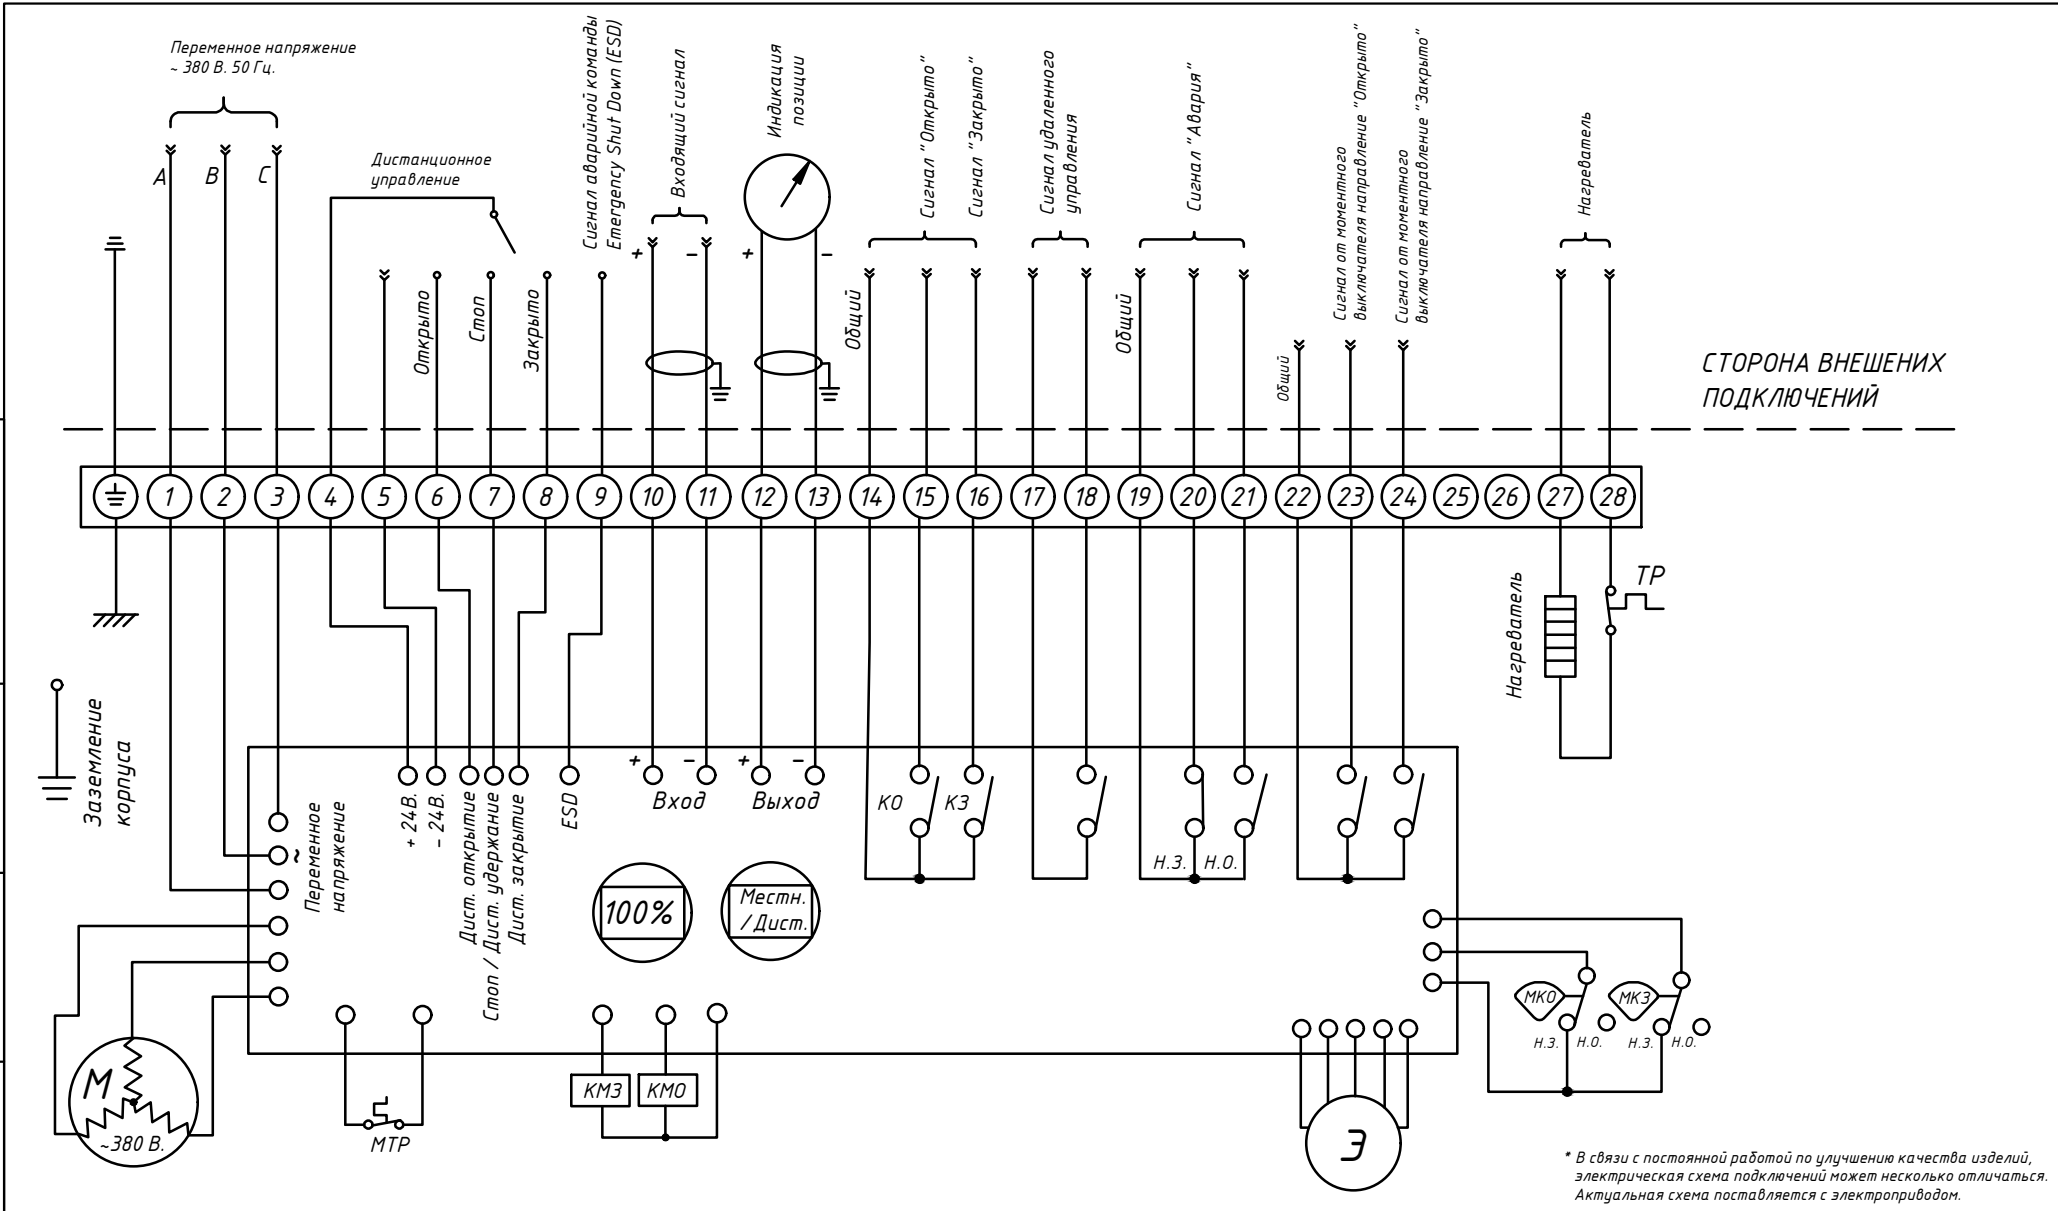

ТР – Термо-реле нагревателя
 МТР – Термо-реле электродвигателя
 М – Электродвигатель
 МКЗ, МКО – Выключатели ограничителя момента
 КЗ, КО – Конечные выключатели
 КМЗ, КМО – Контакторы
 Э – Энкодер

Изм.	Лист	№ докум.	Подп.	Дата
Разраб.	Балашов К.В.			05.23
Пров.				
Н.контр.				
Утв.				

AR21E-287-10

Электрическая схема электропривода AR21E

Напряжение питания: 380В. (переменное).

Режим: Интеллектуальный модуль INT/N

Модельный ряд: AR21E.007-100

Стадия	Лист	Листов
Р	1	1